LEI Nº 1916/2024
DE 29 DE AGOSTO DE 2024

"Dispõe sobre denominação de vias públicas que específica"

PAULO ROGÉRIO PEREIRA, no exercício do cargo de Prefeito Municipal, no uso das atribuições que lhe são conferidas por Lei, faz saber que a **CÂMARA MUNICIPAL** aprovou e eu sanciono a seguinte Lei:

Artigo 1º - As ruas do Loteamento Residencial Recanto da Vovó Zica, localizado no Bairro do Areal, neste Município, passam a denominar-se:

Rua 01 e Rua 2 – Pedro Donizeti Zanardi;
Rua 03 – Odete Fornari de Oliveira Preto; e
Rua 04 – Iracema Camargo Oliveira.

Artigo 2º - Esta Lei entra em vigor na data de sua publicação, revogadas as disposições em contrário.

Pinhalzinho/SP, 29 de agosto de 2024

PAULO ROGÉRIO PEREIRA
Prefeito Municipal de Pinhalzinho/SP

Publicado no Diário Oficial do Município em 29/08/2024 – Edição 927/2024

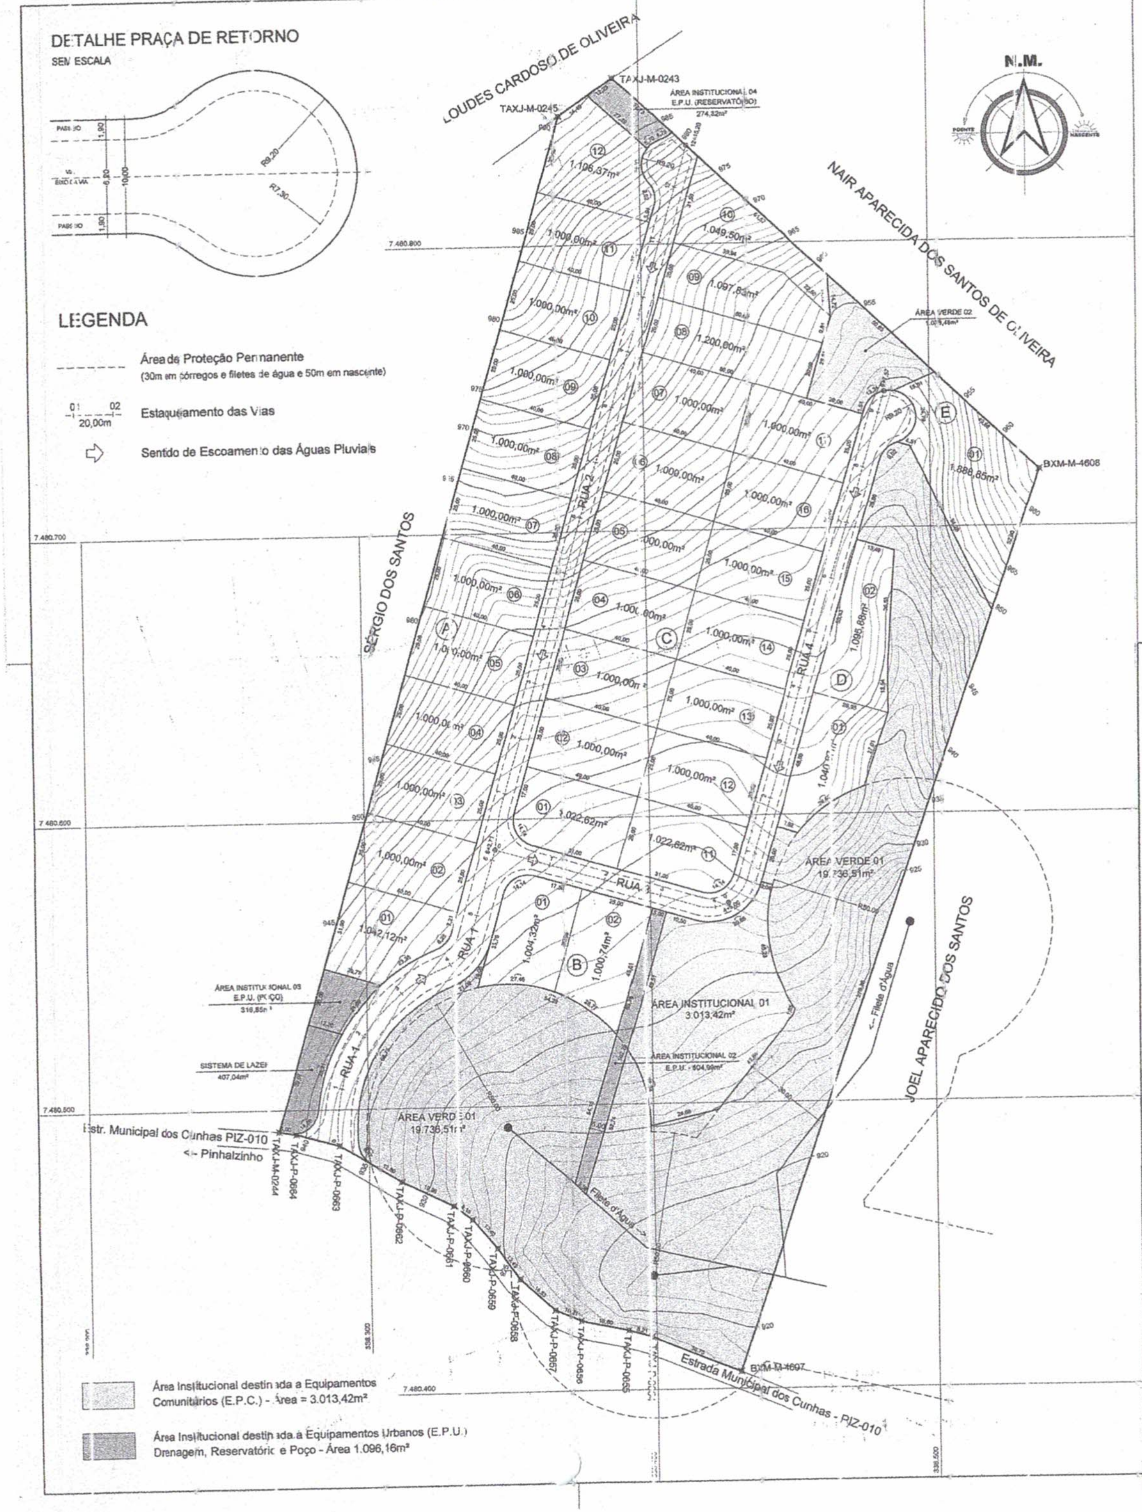
DETALHE PRAÇA DE RETORNO
SEM ESCALA
PASSEIO
VIA
1,90
6,20
10,00
R9,20
R7,30
N.M.
LOUDES CARDOSO DE OLIVEIRA
NAIR APARECIDA DOS SANTOS DE OLIVEIRA
SERGIO DOS SANTOS
JOEL APARECIDO DOS SANTOS
TAXJ-M-0243
TAXJ-M-0245
BXM-M-4608
BXM-M-4607
ÁREA INSTITUCIONAL 04
E.P.U. (RESERVATÓRIO)
274,32m²
ÁREA VERDE 02
ÁREA VERDE 01
19.736,51m²
ÁREA INSTITUCIONAL 01
3.013,42m²
ÁREA INSTITUCIONAL 02
E.P.U. - 504,99m²
ÁREA INSTITUCIONAL 03
E.P.U. (POÇO)
316,85m²
SISTEMA DE LAZER
407,04m²
RUA 1
RUA 2
RUA 3
RUA 4
A
B
C
D
E
1.106,37m²
1.049,50m²
1.097,62m²
1.200,00m²
1.000,00m²
1.888,85m²
1.095,88m²
1.040,73m²
1.022,62m²
1.004,32m²
1.000,74m²
1.042,12m²
<- Filete d'Água
Estr. Municipal dos Cunhas PIZ-010
<- Pinhalzinho
Estrada Municipal dos Cunhas - PIZ-010
TAXJ-M-0244
TAXJ-P-0654
TAXJ-P-0655
TAXJ-P-0656
TAXJ-P-0657
TAXJ-P-0658
TAXJ-P-0659
TAXJ-P-0660
TAXJ-P-0661
TAXJ-P-0662
TAXJ-P-0663
TAXJ-P-0664
7.480.800
7.480.700
7.480.600
7.480.500
7.480.400
338.500

LEGENDA

- Área de Proteção Permanente (30m em córregos e filetes de água e 50m em nascente)
- 01 — 02 20,00m Estaqueamento das Vias
- ⇨ Sentido de Escoamento das Águas Pluviais
- ▨ Área Institucional destinada a Equipamentos Comunitários (E.P.C.) - Área = 3.013,42m²
- ▨ Área Institucional destinada a Equipamentos Urbanos (E.P.U.) Drenagem, Reservatório e Poço - Área 1.096,16m²

Gleba

De	PARA	AZIMUTE	DISTÂNCIA
TAXJ-M-0243	BXM-M-4608	133°56'	205,17m
BXM-M-4608	BXM-M-4607	199°36'	330,36m
BXM-M-4607	TAXJ-P-0654	292°11'	36,75m
TAXJ-P-0654	TAXJ-P-0655	287°12'	8,21m
TAXJ-P-0655	TAXJ-P-0656	282°28'	16,80m
TAXJ-P-0656	TAXJ-P-0657	293°59'	10,21m
TAXJ-P-0657	TAXJ-P-0658	312°48'	16,53m
TAXJ-P-0658	TAXJ-P-0659	325°39'	13,45m
TAXJ-P-0659	TAXJ-P-0660	320°17'	13,40m
TAXJ-P-0660	TAXJ-P-0661	307°24'	8,15m
TAXJ-P-0661	TAXJ-P-0662	296°32'	19,96m
TAXJ-P-0662	TAXJ-P-0663	301°16'	25,67m
TAXJ-P-0663	TAXJ-P-0664	286°05'	15,65m
TAXJ-P-0664	TAXJ-M-0244	279°14'	6,13m
TAXJ-M-0244	TAXJ-M-0245	17°01'	368,00m
TAXJ-M-0245	TAXJ-M-0243	77°58'	26,72m

Área: 68.097,00m²
6,8097 ha

SECÇÃO TRANSVERSAL DAS VIAS

ESCALA 1 : 100

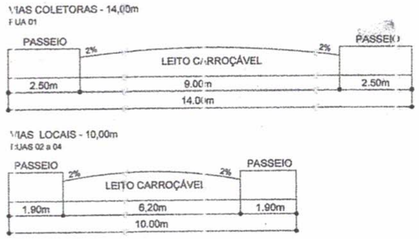
VIAS COLETORAS - 14,00m
RUA 01
PASSEIO
2%
LEITO CARROÇÁVEL
2%
PASSEIO
2.50m
9.00m
2.50m
14.00m
VIAS LOCAIS - 10,00m
RUAS 02 a 04
PASSEIO
2%
LEITO CARROÇÁVEL
2%
PASSEIO
1.90m
6,20m
1.90m
10.00m

PROJETO URBANÍSTICO

FOLHA ÚNICA

PROJETO LOTEAMENTO RESIDENCIAL RECANTO DA VOVÓ ZICA

PROPRIETÁRIO LOTEAMENTO RESID. RECANTO DA VOVÓ ZICA SPE LTDA.
CNPJ Nº 32.314.078/0001-77

LOCAL ESTRADA MUNICIPAL DOS CUNHAS - PIZ-010
BAIRRO DO AREAL - PINHALZINHO-SP

PROTOCOLO
-16225

ESCALA 1:1000

MATRÍCULA nº 95.877 do C.R.I. DE BRAGANÇA PAULISTA-SP

SITUAÇÃO SEM ESCALA

VIDE PLANTA

DECLARAÇÃO

DECLARO QUE A APROVAÇÃO DO PROJETO NÃO IMPLICA A PREFEITURA NO RECONHECIMENTO DO DIREITO DE PROPRIEDADE NO REFERIDO IMÓVEL

Roseni[illegible] Duarte de [illegible] Zanardi
PROPRIETÁRIO
LOTEAMENTO RESIDENCIAL RECANTO DA VOVÓ ZICA SPE LTDA.
CNPJ Nº 32.314.078/0001-77

ÁREAS

1. ÁREA DOS LOTES		
1.1. LOTES RESIDENCIAIS (34 unid.)	35.571,52	52,24
2. ÁREAS PÚBLICAS		
2.1. SISTEMA VIÁRIO	7.263,87	10,67
2.2. ÁREA INSTITUCIONAL (equip. urbanos e san.)	4.109,58	6,03
2.3. ESPAÇOS LIVRES DE USO PÚBLICO		
2.3.1 ÁREAS VERDES	20.744,99	30,46
2.3.2 SISTEMA DE LAZER	407,04	0,60
ÁREA LOTEADA = TOTAL DA GLEBA	68.097,00	100,00

AUTOR DO PROJETO E RESP. TÉCNICO
MARCOS ROBERTO GUARIZZO
ENGENHEIRO CIVIL
CREA 5061638170
ART 28027230191236 HT

Prefeitura Municipal de Pinhalzinho
APROVADO
Nº DO PROCESSO: 3737/2019
DATA DA APROVAÇÃO: 10/06/2019
RESPONSÁVEL:
Edson Lisbôa Carlos
ARQUITETO & URBANISTA
CAU - A65556-9
CHEFE DEPTO. OBRAS

graprohab
APROVADO
Certificado nº 468/19
Lacir Ferreira Baldusco
Presidente