LEI Nº 1.923/2024
DE 19 DE SETEMBRO DE 2024

"Dispõe sobre denominação de vias públicas que especifica"

PAULO ROGÉRIO PEREIRA, no exercício do cargo de Prefeito Municipal, no uso das atribuições que lhe são conferidas por Lei, faz saber que a Câmara Municipal aprovou e eu sanciono a seguinte Lei:

Artigo 1º - As ruas do Loteamento Residencial Chácaras Treviso, localizado no Bairro da Fazenda Velha, neste Município, passam a denominar-se:

Rua 01 – Júlio Antonio de Lima;
Rua 02 – Joana da Rocha Moreira.

Artigo 2º - Esta Lei entra em vigor na data de sua publicação, revogadas as disposições em contrário.

Pinhalzinho, 19 de setembro de 2024.

PAULO ROGÉRIO PEREIRA
Prefeito Municipal

Publicado no Diário Oficial do Município em 20/09/2024 – Edição 943/2024

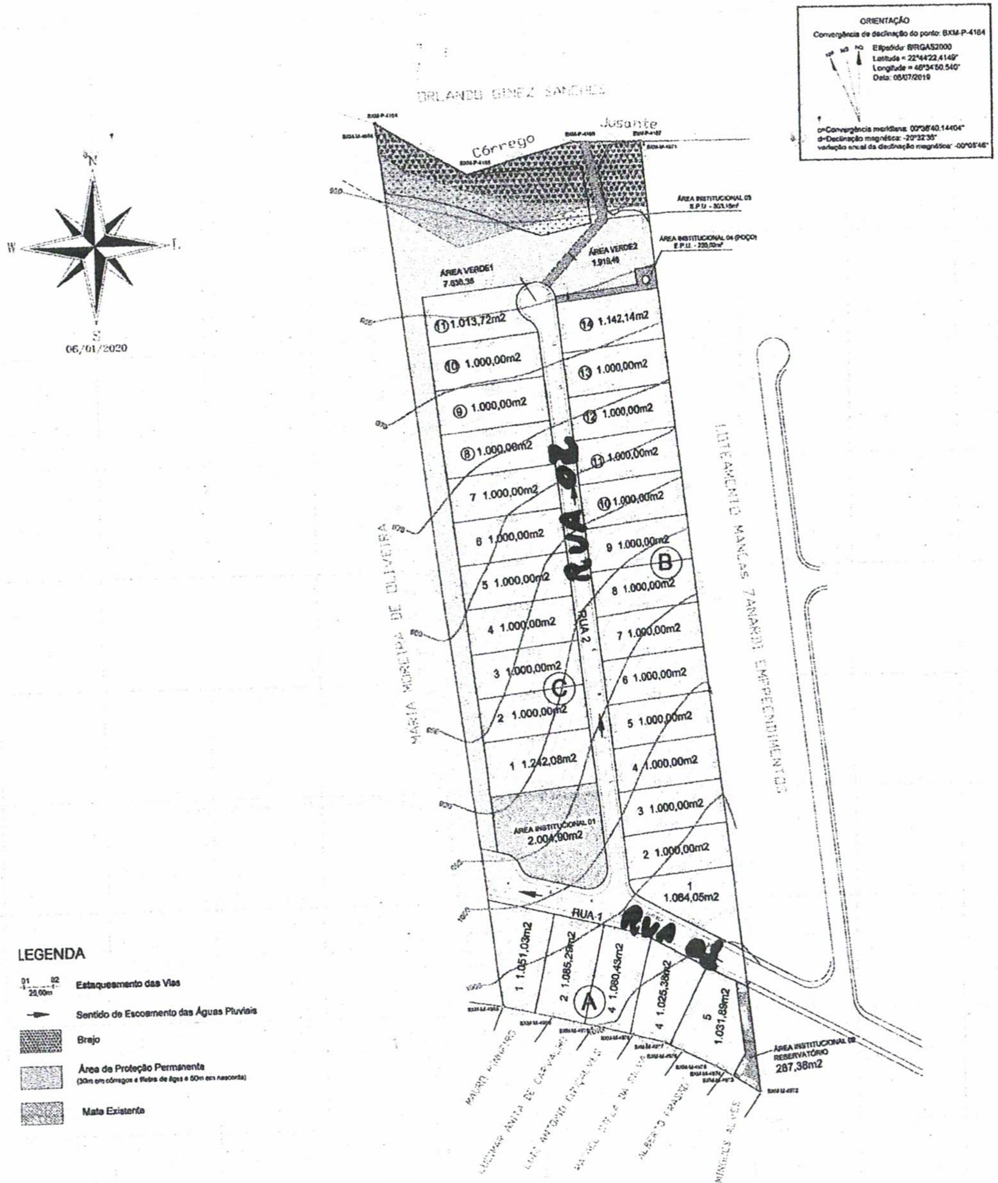

ORIENTAÇÃO
Convergência de declinação do ponto: BXM-P-4164
Elipsóide BIRGAS2000
Latitude = 22°44'22,4149"
Longitude = 46°34'50,540"
Data: 08/07/2019
c=Convergência meridiana: 00°38'40,14404"
d=Declinação magnética: -20°32'35"
variação anual da declinação magnética: -00°05'46"

SECÇÃO TRANSVERSAL DAS VIAS

ESCALA 1 : 100

VIAS COLETORAS - 14.00m
RUAS 01

VIAS LOCAIS - 10,00m
RUAS 02

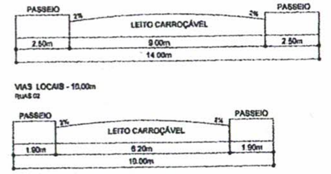

DETALHE PRAÇA DE RETORNO
SEM ESCALA

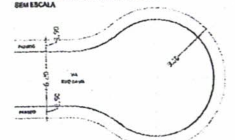

Tabela de Coordenadas – Azimutes – Distâncias					
Ponto	Azimute	Distância(m)	Latitude	Longitude	Altitude
BXM-P-4164 – BXM-P-4165	123°04'00"	47,07	-22°44'22,984"	-46°34'49,158"	955,27
BXM-P-4165 – BXM-P-4166	74°24'00"	51,05	-22°44'22,538"	-46°34'47,435"	955,22
BXM-P-4166 – BXM-P-4167	91°35'00"	33,14	-22°44'22,568"	-46°34'46,274"	956,68
BXM-P-4167 – BXM-M-4971	174°15'00"	3,43	-22°44'22,679"	-46°34'46,268"	956,68
BXM-M-4971 – BXM-M-4972	174°07'00"	429,03	-22°44'36,551"	-46°34'44,725"	1014,08
BXM-M-4972 – BXM-M-4973	302°00'00"	14,98	-22°44'36,293"	-46°34'45,170"	1015,81
BXM-M-4973 – BXM-M-4974	300°17'00"	4,33	-22°44'36,222"	-46°34'45,301"	1015,07
BXM-M-4974 – BXM-M-4975	300°03'00"	4,91	-22°44'36,142"	-46°34'45,450"	1014,45
BXM-M-4975 – BXM-M-4976	295°58'00"	16,79	-22°44'35,903"	-46°34'45,979"	1014,27
BXM-M-4976 – BXM-M-4977	295°52'00"	9,52	-22°44'35,768"	-46°34'46,279"	1013,58
BXM-M-4977 – BXM-M-4978	283°49'00"	16,22	-22°44'35,642"	-46°34'46,831"	1012,17
BXM-M-4978 – BXM-M-4979	283°42'00"	20,00	-22°44'35,488"	-46°34'47,512"	1010,97
BXM-M-4979 – BXM-M-4980	283°47'00"	20,01	-22°44'35,333"	-46°34'48,193"	1009,65
BXM-M-4980 – BXM-M-4985	283°46'00"	23,39	-22°44'35,152"	-46°34'48,989"	1008,77
BXM-M-4985 – BXM-M-4984	353°41'00"	397,89	-22°44'22,304"	-46°34'50,681"	957,66
BXM-M-4984 – BXM-P-4164	353°30'00"	4,80	-22°44'22,149"	-46°34'50,540"	937,66

Área m2.	Área Ha.	Área Alq.	Perímetro m.
47.880,00	4,788	1,970	1097,84

PROJETO URBANÍSTICO

FOLHA ÚNICA

PROTOCOLO Nº
-17451
GRAPROHAB

PROJETO RESIDENCIAL CHÁCARAS TREVISO

PROPRIETÁRIO R. RIBEIRO & GOMES NETO EMPREENDIMENTOS IMOBILIÁRIOS SPE LTDA

LOCAL ESTRADA MUNICIPAL PIZ-435, BAIRRO FAZENDA VELHA
PINHALZINHO - SP

ESCALA 1:1000 MATRÍCULA 96.309 C.R.I DA COMARCA DE BRAGANÇA PAULISTA

SITUAÇÃO SEM ESCALA

VIDE PLANTA

ÁREAS	m²	%
1. ÁREA DOS LOTES		
1.1. LOTES RESIDENCIAIS (30 UN.)	30.726,01	64,43
2. ÁREAS PÚBLICAS		
2.1 SISTEMA VIÁRIO	4.677,28	9,80
2.2. ÁREA INSTITUCIONAL [illegible]	2.815,45	5,89
2.3. ESPAÇOS LIVRES DE USO PÚBLICO		
2.3.1 ÁREAS VERDES	9.557,24	20,04
ÁREA LOTEADA = TOTAL DA GLEBA	47.880,00	100,00

DECLARAÇÃO
DECLARO QUE A APROVAÇÃO DO PROJETO NÃO IMPLICA A PREFEITURA NO RECONHECIMENTO DO DIREITO DE PROPRIEDADE NO REFERIDO IMÓVEL

PROPRIETÁRIO
R. RIBEIRO & GOMES NETO EMPREENDIMENTOS IMOBILIÁRIOS SPE LTDA

AUTOR DO PROJETO E RESP. TÉCNICO
LUIS AUGUSTO DE PAULA
ENGENHEIRO CIVIL
CREA-SP [illegible]
ART: [illegible]

Prefeitura Municipal de Pinhalzinho
APROVADO
Nº DO PROCESSO: 1230/2021
DATA DA APROVAÇÃO: 23/12/2021
RESPONSÁVEL:

graprohab
APROVADO
Certificado nº 294/21
Lacir Ferreira Baldusco
Presidente

LEGENDA

- 01 02 20,00m Estaqueamento das Vias
- → Sentido de Escoamento das Águas Pluviais
- ▨ Brejo
- ▨ Área de Proteção Permanente (30m em córregos e filetes de água e 50m em nascente)
- ▨ Mata Existente

Convenções Topográficas

- ▨ Área Institucional 01 destinada a Equipamentos Públicos Comunitários (E.P.C.) - Área = 2.004,90m²
- ▨ Área Institucional 02 a 04 destinadas a Equipamentos Públicos Urbanos (E.P.U.) Redes, Reservatório e Poço - 810,65m²