LEI Nº 1.997/2025
DE 27 DE AGOSTO DE 2025

"Dispõe sobre denominação de vias públicas que especifica"

SEBASTIÃO ZANARDI, no exercício do cargo de Prefeito Municipal, no uso das atribuições que lhe são conferidas por Lei, faz saber que a Câmara Municipal aprovou e eu sanciono a seguinte Lei:

Artigo 1º - As ruas do Loteamento Residencial **Jardim Violeta,** no Bairro da Rosa Mendes, neste Município**,** conforme memorial descritivo anexo**,** passam a denominar-se:


- **Rua 1 – Dália;**
- **Rua 2 – Lótus;**
- **Rua 3 – Amarílis;**
- **Rua 4 – Lobelia;**
- **Rua 5 - Petúnia;**

Artigo 2º - Esta Lei entra em vigor na data de sua publicação, revogadas as disposições em contrário.

Pinhalzinho, 27 de agosto de 2025.

Sebastião Zanardi
Prefeito do Município

Publicado no Diário Oficial do Município em 27/08/2025 – Edição 1177/2025.

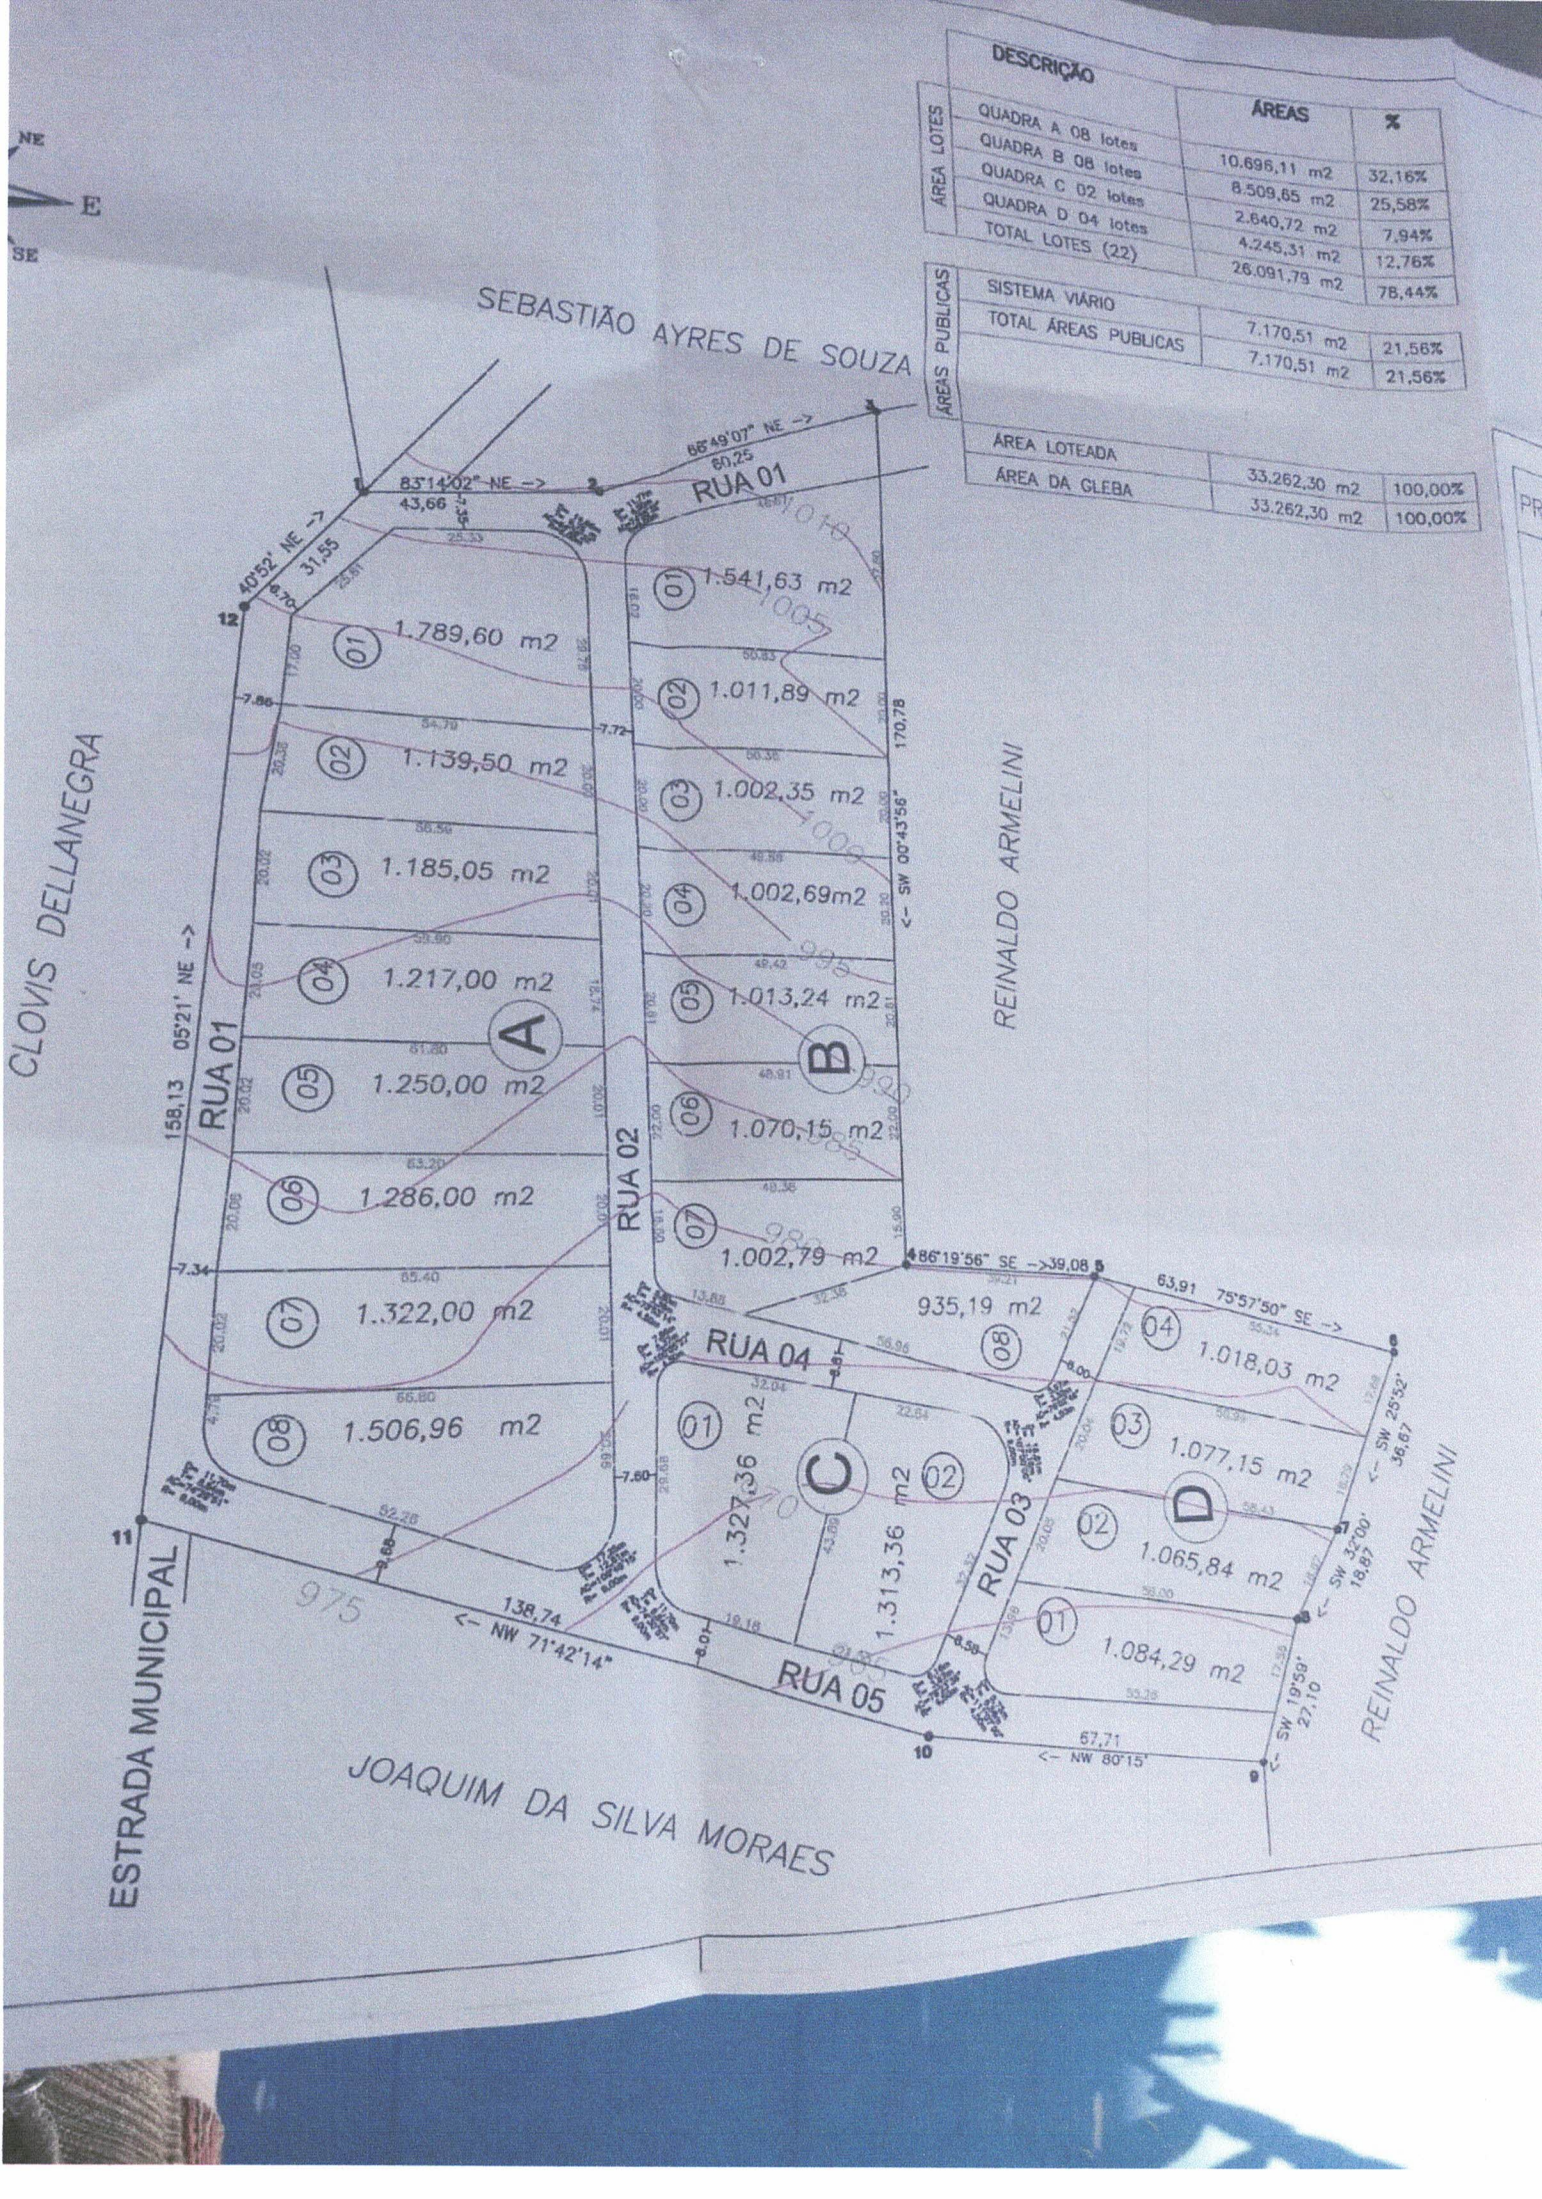

DESCRIÇÃO		ÁREAS	%
ÁREA LOTES	QUADRA A 08 lotes	10.696,11 m2	32,16%
	QUADRA B 08 lotes	8.509,65 m2	25,58%
	QUADRA C 02 lotes	2.640,72 m2	7,94%
	QUADRA D 04 lotes	4.245,31 m2	12,76%
	TOTAL LOTES (22)	26.091,79 m2	78,44%
ÁREAS PUBLICAS	SISTEMA VIÁRIO	7.170,51 m2	21,56%
	TOTAL ÁREAS PUBLICAS	7.170,51 m2	21,56%
	ÁREA LOTEADA	33.262,30 m2	100,00%
	ÁREA DA GLEBA	33.262,30 m2	100,00%