LEI Nº 1.926/2024
DE 19 DE SETEMBRO DE 2024

"Dispõe sobre denominação de vias públicas que especifica"

PAULO ROGÉRIO PEREIRA, no exercício do cargo de Prefeito Municipal, no uso das atribuições que lhe são conferidas por Lei, faz saber que a Câmara Municipal aprovou e eu sanciono a seguinte Lei:

Artigo 1º - As ruas do Loteamento Residencial Bela Vista, localizado no Bairro Jardim do Limão, neste Município, passam a denominar-se:

Rua 01 – Luiz Gracelino Teixeira (continuação)
Rua 02 – Luiz Gasolla;
Rua 03 – Sargento PM Laércio Mendes;
Rua 04 – Salvador Ribeiro Alves (Coca);
Rua 05 – Luiz Gonzaga de Godoi (Luizinho); e
Rua 06 – Hugo Ramos.

Artigo 2º - Esta Lei entra em vigor na data de sua publicação, revogadas as disposições em contrário.

Pinhalzinho, 19 de setembro de 2024.

PAULO ROGÉRIO PEREIRA
Prefeito Municipal

Publicado no Diário Oficial do Município em 20/09/2024 – Edição 943/2024

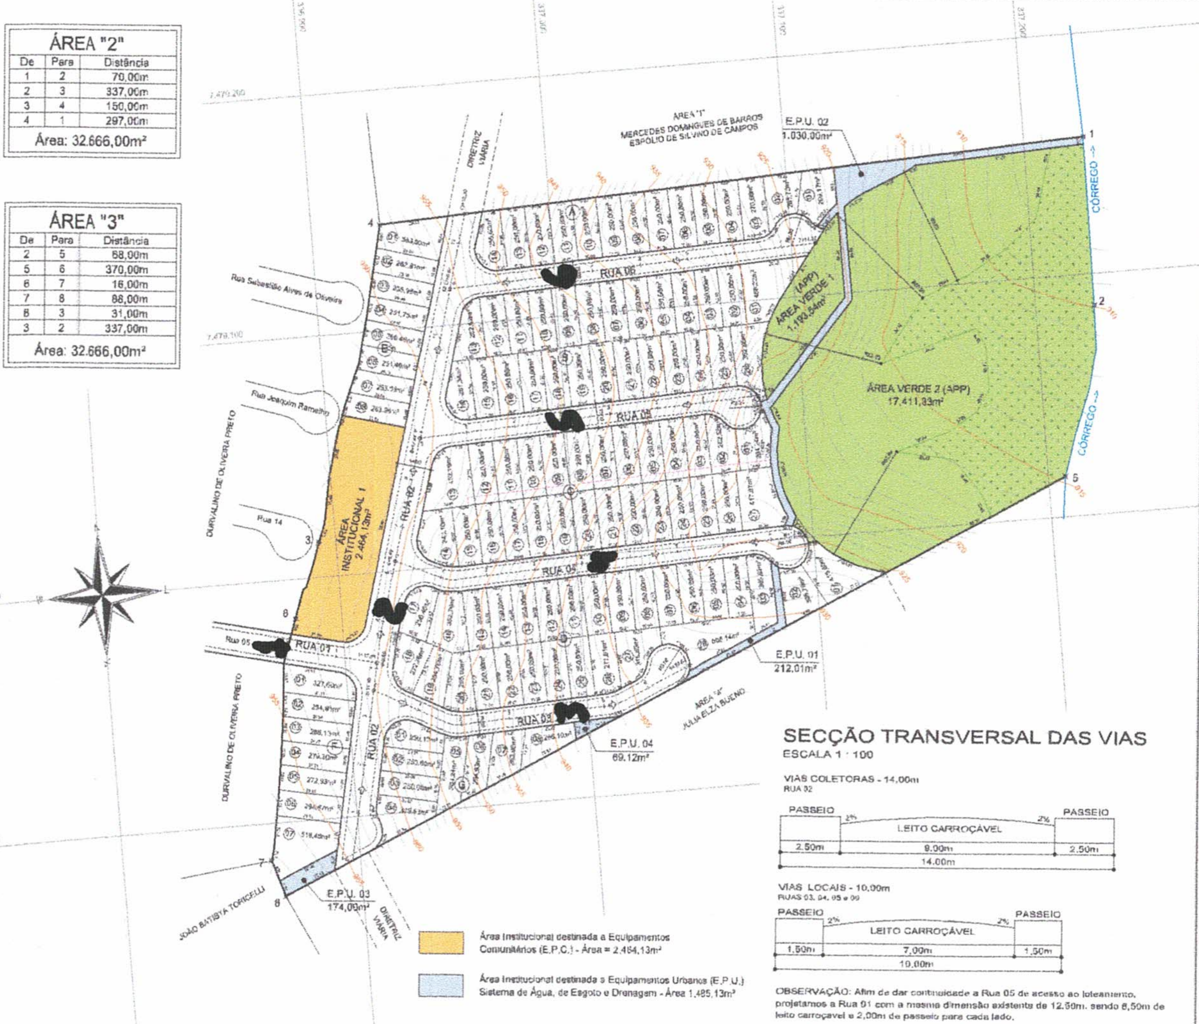
CÓRREGO
1
2
3
4
5
6
7
8
ÁREA VERDE 2 (APP) 17.411,83m²
ÁREA VERDE 1 (APP) 1.190,54m²
ÁREA INSTITUCIONAL 1 2.464,13m²
E.P.U. 01 212,01m²
E.P.U. 02 1.030,00m²
E.P.U. 03 174,00m²
E.P.U. 04 69,12m²
RUA 01
RUA 02
RUA 03
RUA 04
RUA 05
RUA 06
Rua 05
Rua 14
Rua Sebastião Alves de Oliveira
Rua Joaquim Ramalho
DURVALINO DE OLIVEIRA PRETO
JOÃO BATISTA TORICELLI
DIRETRIZ VIÁRIA
ÁREA "1" MERCEDES DOMINGUES DE BARROS ESPÓLIO DE SILVINO DE CAMPOS
ÁREA "4" JULIA ELZA BUENO
L

ÁREA "2"

De	Para	Distância
1	2	70,00m
2	3	337,00m
3	4	150,00m
4	1	297,00m
Área: 32.666,00m²		

ÁREA "3"

De	Para	Distância
2	5	68,00m
5	6	370,00m
6	7	16,00m
7	8	88,00m
8	3	31,00m
3	2	337,00m
Área: 32.666,00m²		

🟧 Área Institucional destinada a Equipamentos Comunitários (E.P.C.) - Área = 2.464,13m²

🟦 Área Institucional destinada a Equipamentos Urbanos (E.P.U.) Sistema de Água, de Esgoto e Drenagem - Área 1.485,13m²

SECÇÃO TRANSVERSAL DAS VIAS

ESCALA 1 : 100

VIAS COLETORAS - 14,00m
RUA 02

PASSEIO	LEITO CARROÇÁVEL	PASSEIO
2,50m	9,00m	2,50m
14,00m		

2% 2%

VIAS LOCAIS - 10,00m
RUAS 03, 04, 05 e 06

PASSEIO	LEITO CARROÇÁVEL	PASSEIO
1,50m	7,00m	1,50m
10,00m		

2% 2%

OBSERVAÇÃO: Afim de dar continuidade a Rua 05 de acesso ao loteamento, projetamos a Rua 01 com a mesma dimensão existente de 12,50m, sendo 8,50m de leito carroçável e 2,00m de passeio para cada lado.

LEGENDA

- 01 – 02 / 20,00m — ESTAQUEAMENTO DAS VIAS
- FAIXA NON AEDIFICANDI - 3 metros
- ⇨ SENTIDO DE ESCOAMENTO DE ÁGUAS PLUVIAIS
- 🟩 Área de Proteção Permanente (30m em córregos e filetes de água e 50m em nascente e borda de áreas alagadiças)
- ▨ Brejo

PROJETO URBANÍSTICO

FOLHA ÚNICA

PROJETO LOTEAMENTO RESIDENCIAL BELA VISTA

PROPRIETÁRIAS D. FORNARI & CIA LTDA-ME

PROTOCOLO Nº
14389.
GRAPROHAB

LOCAL ÁREA NÚMERO "2" E "3" - BAIRRO DO PINHAL
PINHALZINHO-SP

ESCALA 1:1000 MATRÍCULAS 39.227 e 39.229 - C.R.I. BRAGANÇA PAULISTA-SP

SITUAÇÃO SEM ESCALA

VIDE PLANTA

ÁREAS

ÁREAS	m²	%
ÁREA DOS LOTES		
LOTES RESIDENCIAIS (115 unid.)	32.051,84	49,06
SUB TOTAL 1 (115 unid.)	32.051,84	49,06
ÁREAS PÚBLICAS		
SISTEMA VIÁRIO	10.726,23	16,42
ÁREA INSTITUCIONAL (equip. urbanos e com.)	3.949,29	6,04
SUB TOTAL 2	14.675,49	22,46
ESPAÇOS LIVRES DE USO PÚBLICO		
ÁREAS VERDES	18.604,37	28,48
SUB TOTAL 3	18.604,37	28,48
ÁREA LOTEADA = TOTAL DA GLEBA	[illegible]	100,00

DECLARAÇÃO

DECLARO QUE A APROVAÇÃO DO PROJETO NÃO IMPLICA A PREFEITURA NO RECONHECIMENTO DO DIREITO DE PROPRIEDADE NO REFERIDO IMÓVEL

PROPRIETÁRIO
D. FORNARI & CIA LTDA-ME

AUTOR DO PROJETO E RESP. TÉCNICO
MARCOS ROBERTO GUARIZZO
ENGENHEIRO CIVIL
CREA [illegible]
ART [illegible]

ARQUITETO & URBANISTA
CHEFE DEPTO OBRAS

APROVADO
Em 04/06/18
PREFEITURA MUNICIPAL DE PINHALZINHO

graprohab
APROVADO
Certificado nº 351/17
Lacir Ferreira Baldusco
Presidente