LEI Nº 1911/2024
DE 16 DE JULHO DE 2024

"Dispõe sobre denominação de vias públicas que específica"

PAULO ROGÉRIO PEREIRA, no exercício do cargo de Prefeito Municipal, no uso das atribuições que lhe são conferidas por Lei, faz saber que a **CÂMARA MUNICIPAL** aprovou e eu sanciono a seguinte Lei:

Artigo 1º - As ruas do Loteamento Residencial Vento Forte passam a denominar-se:

Rua 01 – Ari de Oliveira Bitello;
Rua 02 – Geraldo Ferreira da Silva;
Rua 03 – Antonio Luiz de Almeida; e
Rua 04 – Luiz Gonçalves de Freitas.

Artigo 2º - Esta Lei entra em vigor na data de sua publicação, revogadas as disposições em contrário.

Pinhalzinho/SP, 16 de julho de 2024

PAULO ROGÉRIO PEREIRA
Prefeito Municipal de Pinhalzinho/SP

Publicado no Diário Oficial do Município em 16/07/2024 – Edição 883/2024

PROJETO DO SISTEMA VIÁRIO

FOLHA ÚNICA

PROJETO LOTEAMENTO RESIDENCIAL VENTO FORTE

PROPRIETÁRIO LAURINDO SERRANO E OUTROS
CPF nº 610.058.278-34

LOCAL Sítio Vento Forte, Estrada Municipal PIZ-435
Bairro da Fazenda Velha - Pinhalzinho - SP

ESCALA 1:1000

MATRÍCULA 95.095 DO C.R.I DA COMARCA DE BRAGANÇA PAULISTA-SP

SITUAÇÃO SEM ESCALA

VIDE PLANTA

DECLARAÇÃO

DECLARO QUE A APROVAÇÃO DO PROJETO NÃO IMPLICA A PREFEITURA NO RECONHECIMENTO DO DIREITO DE PROPRIEDADE NO REFERIDO IMÓVEL

Laurindo Serrano
PROPRIETÁRIO
LAURINDO SERRANO
CPF nº 610.058.278-34

ÁREAS

ÁREAS	m^2	%
1. ÁREA DOS LOTES		
1.1. LOTES RESIDENCIAIS (68 unid.)	72.387,76	61,67
2. ÁREAS PÚBLICAS		
2.1. SISTEMA VIÁRIO	11.955,67	10,18
2.2. ÁREA INSTITUCIONAL (Equip. Urb. e Comun.)	7.052,48	6,01
2.3. ESPAÇOS LIVRES DE USO PÚBLICO		
2.3.1 ÁREAS VERDES	22.516,87	19,18
2.3.2 SISTEMA DE LAZER	3.468,22	2,96
ÁREA LOTEADA = TOTAL DA GLEBA	117.381,00	100,00

AUTOR DO PROJETO E RESP. TÉCNICO
MARCOS ROBERTO GUARIZZO
ENGENHEIRO CIVIL
CREA 5061638170
ART 28027230181115654

APROVADO
EM 31 / 10 /20 19
PREFEITURA MUNICIPAL DE PINHALZINHO

Edson Lisboa S. Santos
ARQTO. E URBANISTA
CAU - A68556-9
CHEFE DO DEPTO. DE OBRAS

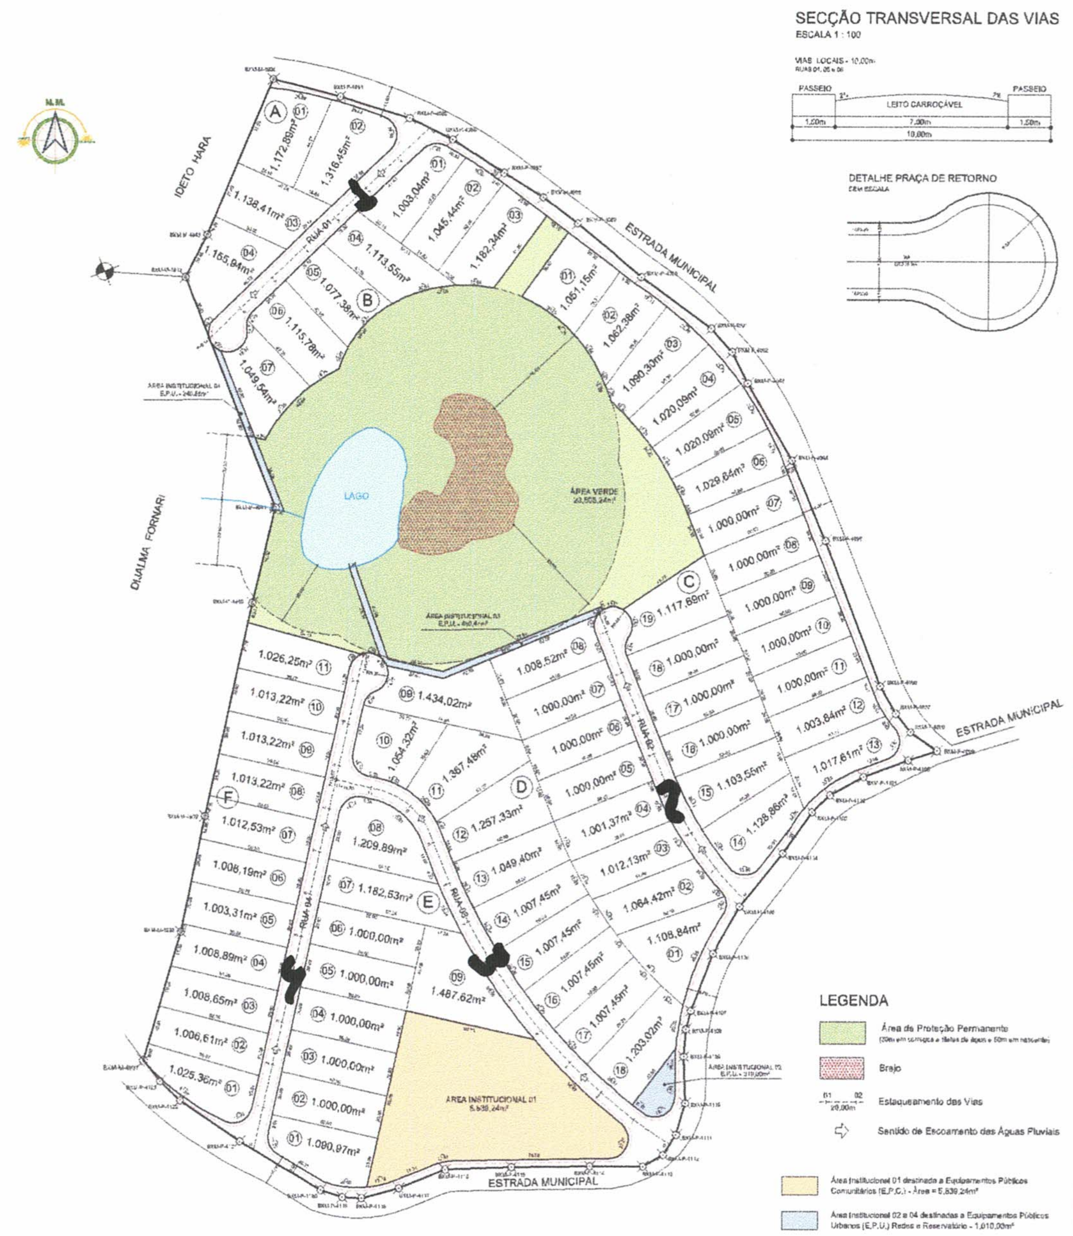

SECÇÃO TRANSVERSAL DAS VIAS

ESCALA 1 : 100

DETALHE PRAÇA DE RETORNO

SEM ESCALA

LEGENDA

- 🟩 Área de Proteção Permanente (30m em córregos e faixas de água e 50m em nascentes)
- ▨ Brejo
- 01 — 02, 20,00m: Estaqueamento das Vias
- ⇨ Sentido de Escoamento das Águas Pluviais
- 🟨 Área Institucional 01 destinada a Equipamentos Públicos Comunitários (E.P.C.) - Área = 5.839,24m²
- 🟦 Área Institucional 02 e 04 destinadas a Equipamentos Públicos Urbanos (E.P.U.) Redes e Reservatório - 1.010,00m²

Sítio Vento Forte

De	Latitude	Longitude	Para	Azim. 3°Ed.	Dist. 3°Ed.
BXM-M-4936	-22°44'39,346"	-46°34'35,064"	BXM-P-4084	106°02'	32,12 m
BXM-P-4084	-22°44'39,619"	-46°34'34,997"	BXM-P-4085	107°27'	33,44 m
BXM-P-4085	-22°44'39,945"	-46°34'33,879"	BXM-P-4086	117°09'	22,94 m
BXM-P-4086	-22°44'40,272"	-46°34'33,192"	BXM-P-4087	123°49'	28,93 m
BXM-P-4087	-22°44'40,779"	-46°34'32,376"	BXM-P-4088	121°49'	21,36 m
BXM-P-4088	-22°44'41,145"	-46°34'31,740"	BXM-P-4089	127°14'	20,18 m
BXM-P-4089	-22°44'41,542"	-46°34'31,177"	BXM-P-4090	129°54'	28,80 m
BXM-P-4090	-22°44'42,351"	-46°34'30,134"	BXM-P-4091	126°26'	26,52 m
BXM-P-4091	-22°44'43,114"	-46°34'29,020"	BXM-P-4092	138°58'	14,77 m
BXM-P-4092	-22°44'43,476"	-46°34'28,690"	BXM-P-4093	154°06'	16,01 m
BXM-P-4093	-22°44'43,944"	-46°34'28,436"	BXM-P-4094	156°06'	41,06 m
BXM-P-4094	-22°44'45,101"	-46°34'27,716"	BXM-P-4095	157°04'	40,98 m
BXM-P-4095	-22°44'46,301"	-46°34'27,171"	BXM-P-4096	158°16'	71,33 m
BXM-P-4096	-22°44'48,470"	-46°34'26,206"	BXM-P-4097	156°30'	14,67 m
BXM-P-4097	-22°44'48,886"	-46°34'26,036"	BXM-P-4098	141°26'	10,90 m
BXM-P-4098	-22°44'49,162"	-46°34'25,797"	BXM-P-4099	125°15'	14,92 m
BXM-P-4099	-22°44'49,442"	-46°34'25,370"	BXM-P-4100	251°46'	14,06 m
BXM-P-4100	-22°44'49,585"	-46°34'25,829"	BXM-P-4101	250°32'	22,06 m
BXM-P-4101	-22°44'49,824"	-46°34'26,567"	BXM-P-4102	242°26'	17,96 m
BXM-P-4102	-22°44'50,094"	-46°34'27,125"	BXM-P-4103	227°05'	11,30 m
BXM-P-4103	-22°44'50,344"	-46°34'27,415"	BXM-P-4104	216°46'	23,31 m
BXM-P-4104	-22°44'50,951"	-46°34'27,904"	BXM-P-4105	219°28'	31,50 m
BXM-P-4105	-22°44'51,744"	-46°34'28,608"	BXM-P-4106	210°14'	24,92 m
BXM-P-4106	-22°44'52,441"	-46°34'29,046"	BXM-P-4107	202°16'	27,86 m
BXM-P-4107	-22°44'53,279"	-46°34'29,416"	BXM-P-4108	196°16'	8,77 m
BXM-P-4108	-22°44'53,554"	-46°34'29,497"	BXM-P-4109	184°39'	12,68 m
BXM-P-4109	-22°44'53,964"	-46°34'29,533"	BXM-P-4110	179°00'	21,36 m
BXM-P-4110	-22°44'54,658"	-46°34'29,520"	BXM-P-4111	185°43'	15,05 m
BXM-P-4111	-22°44'55,120"	-46°34'29,663"	BXM-P-4112	212°37'	10,96 m
BXM-P-4112	-22°44'55,428"	-46°34'29,870"	BXM-P-4113	240°35'	10,71 m
BXM-P-4113	-22°44'55,600"	-46°34'30,197"	BXM-P-4114	270°37'	25,08 m
BXM-P-4114	-22°44'55,591"	-46°34'31,076"	BXM-P-4115	269°54'	36,61 m
BXM-P-4115	-22°44'55,593"	-46°34'32,359"	BXM-P-4116	268°29'	30,40 m
BXM-P-4116	-22°44'55,619"	-46°34'33,424"	BXM-P-4117	246°21'	22,93 m
BXM-P-4117	-22°44'55,894"	-46°34'34,171"	BXM-P-4118	250°40'	17,79 m
BXM-P-4118	-22°44'56,037"	-46°34'34,775"	BXM-P-4119	272°55'	9,06 m
BXM-P-4119	-22°44'56,022"	-46°34'35,092"	BXM-P-4120	298°40'	10,57 m
BXM-P-4120	-22°44'55,812"	-46°34'35,448"	BXM-P-4121	301°27'	43,69 m
BXM-P-4121	-22°44'55,171"	-46°34'36,749"	BXM-P-4122	304°18'	23,82 m
BXM-P-4122	-22°44'54,955"	-46°34'37,722"	BXM-P-4123	313°53'	12,87 m
BXM-P-4123	-22°44'54,266"	-46°34'38,047"	BXM-M-4937	321°29'	12,19 m
BXM-M-4937	-22°44'53,955"	-46°34'38,313"	BXM-M-4938	18°56'	61,43 m
BXM-M-4938	-22°44'52,045"	-46°34'37,686"	BXM-M-4939	12°25'	54,41 m
BXM-M-4939	-22°44'50,316"	-46°34'37,276"	BXM-M-4940	13°05'	99,98 m
BXM-M-4940	-22°44'47,155"	-46°34'36,462"	BXM-M-4941	14°08'	44,90 m
BXM-M-4941	-22°44'45,736"	-46°34'36,097"	BXM-M-4942	336°45'	113,81 m
BXM-M-4942	-22°44'42,206"	-46°34'37,542"	BXM-M-4943	26°02'	21,86 m
BXM-M-4943	-22°44'41,661"	-46°34'37,182"	BXM-M-4936	23°45'	77,76 m

Área (SGL): 117.391,00 m²
11,7391 ha
4,8505 Alqs

Perímetro (Cart.): 1.440,709 m

PROJETO URBANÍSTICO

FOLHA ÚNICA

PROJETO LOTEAMENTO RESIDENCIAL VENTO FORTE

PROPRIETÁRIO LAURINDO SERRANO
CPF nº [illegible]

LOCAL Sítio Vento Forte, Estrada Municipal
Bairro da Fazenda Velha - Pinhalzinho - SP

ESCALA 1:1000

MATRÍCULA [illegible] DO C.R.I DA COMARCA DE BRAGANÇA PAULISTA-SP

SITUAÇÃO SEM ESCALA

VIDE PLANTA

ÁREAS

ÁREAS	m²	%
1. [illegible]		
1.1. LOTES RESIDENCIAIS (68 unid.)	[illegible]	[illegible]
SUB TOTAL ITEM 1 (68 unid.)	[illegible]	[illegible]
2. ÁREAS PÚBLICAS		
2.1. SISTEMA VIÁRIO	[illegible]	[illegible]
2.2. ÁREA INSTITUCIONAL (Equip. Urb. e Comun.)	[illegible]	[illegible]
SUB TOTAL ITEM 2.1 E 2.2	[illegible]	[illegible]
2.3. ESPAÇOS LIVRES DE USO PÚBLICO		
2.3.1 ÁREAS VERDES	[illegible]	[illegible]
SUB TOTAL ITEM 2.3	[illegible]	[illegible]
SUB TOTAL ITEM 2	[illegible]	[illegible]
3. OUTROS		
3.1 LAGOS	[illegible]	[illegible]
SUB TOTAL ITEM 3	[illegible]	[illegible]
ÁREA LOTEADA = TOTAL DA GLEBA	[illegible]	[illegible]

DECLARAÇÃO

DECLARO QUE A APROVAÇÃO DO PROJETO NÃO IMPLICA A PREFEITURA NO RECONHECIMENTO DO DIREITO DE PROPRIEDADE NO REFERIDO IMÓVEL

PROPRIETÁRIO
LAURINDO SERRANO
CPF [illegible]

[illegible]
MARCOS ROBERTO GUARIZZO
[illegible]
CREA [illegible]
ART [illegible]