-

LEI Nº 1917/2024
DE 29 DE AGOSTO DE 2024

"Dispõe sobre denominação de vias públicas que específica"

PAULO ROGÉRIO PEREIRA, no exercício do cargo de Prefeito Municipal, no uso das atribuições que lhe são conferidas por Lei, faz saber que a **CÂMARA MUNICIPAL** aprovou e eu sanciono a seguinte Lei:

Artigo 1º - As Ruas do Loteamento Residencial Vista dos Pinheiros II, localizado no Bairro do Matão, neste Município, passam a denominar-se:

- Rua 1 – Benvinda Gomes de Souza (Vozinha);
- Rua 2 – José Soares Pereira (Vôzinho);
- Rua 3 – Nicolau João Macario (Bigode);
- Rua 4 – Rosa Sebastiana Couto (Rosinha);
- Rua 5 – Benedito Aparecido Godoi;
- Rua 6 – José Cazzo Toricelli (Zé Nacreto);
- Rua 7 – Vanderlei Antonio Carradori.

Artigo 2º - Esta Lei entra em vigor na data de sua publicação, revogadas as disposições em contrário.

Pinhalzinho/SP, 29 de agosto de 2024

PAULO ROGÉRIO PEREIRA
Prefeito Municipal de Pinhalzinho/SP

Publicado no Diário Oficial do Município em 29/08/2024 – Edição 927/2024

PROJETO SISTEMA VIÁRIO

FOLHA ÚNICA

PROJETO LOTEAMENTO RESIDENCIAL VISTA DOS PINHEIROS II

PROPRIETÁRIO PINHAL 2 - EMPREENDIMENTOS SPE LTDA
CNPJ nº 28.944.518/0001-85

LOCAL Estrada Municipal Vicente de Araújo
Bairro do Matão - Pinhalzinho - SP

ESCALA 1:1000

MATRÍCULA Nº 73.566 DO C.R.I DA COMARCA DE BRAGANÇA PAULISTA-SP

SITUAÇÃO SEM ESCALA

VIDE PLANTA

DECLARAÇÃO

DECLARO QUE A APROVAÇÃO DO PROJETO NÃO IMPLICA A PREFEITURA NO RECONHECIMENTO DO DIREITO DE PROPRIEDADE NO REFERIDO IMÓVEL

PROPRIETÁRIO
PINHAL 2 - EMPREENDIMENTOS SPE LTDA
ANDRÉ TOSCANO BONDANÇA
CPF nº 818.838.788-00

AUTOR DO PROJETO E RESPONSÁVEL
MARCOS ROBERTO GUARIZZO
ENGENHEIRO CIVIL
CREA 5061634170
ART 28027320191243930

ÁREAS	m²	%
1. ÁREA DOS LOTES		
1.1. LOTES RESIDENCIAIS (342 unid.)	46.309,74	51,75
2. ÁREAS PÚBLICAS		
2.1. SISTEMA VIÁRIO	21.821,82	22,91
2.2. ÁREA INSTITUCIONAL (Equip. Urb. e Comun.)	4.788,49	5,02
2.3. ESPAÇOS LIVRES DE USO PÚBLICO		
2.3.1 ÁREAS VERDES	15.523,55	16,29
2.3.2 SISTEMA DE LAZER	3.842,47	4,03
ÁREA LOTEADA = TOTAL DA GLEBA	95.284,47	100,00

Prefeitura Municipal de Pinhalzinho
APROVADO
Nº DO PROCESSO: 70/21
DATA DA APROVAÇÃO: 08/07/2021
RESPONSÁVEL:

João Francisco Mangolim
ENGENHEIRO CIVIL
CREA: 060120220

Edson Lisboa Santos
ARQUITETO & URBANISTA
CAU - A88536-9
CHEFE DEPTO. OBRAS

SECÇÃO TRANSVERSAL DAS VIAS


ESCALA 1 : 100

VIAS COLETORAS - 14,00m
RUAS 01 e 02

VIAS LOCAIS - 10,00m
RUAS 05 a 07

DETALHE PRAÇA DE RETORNO

SEM ESCALA

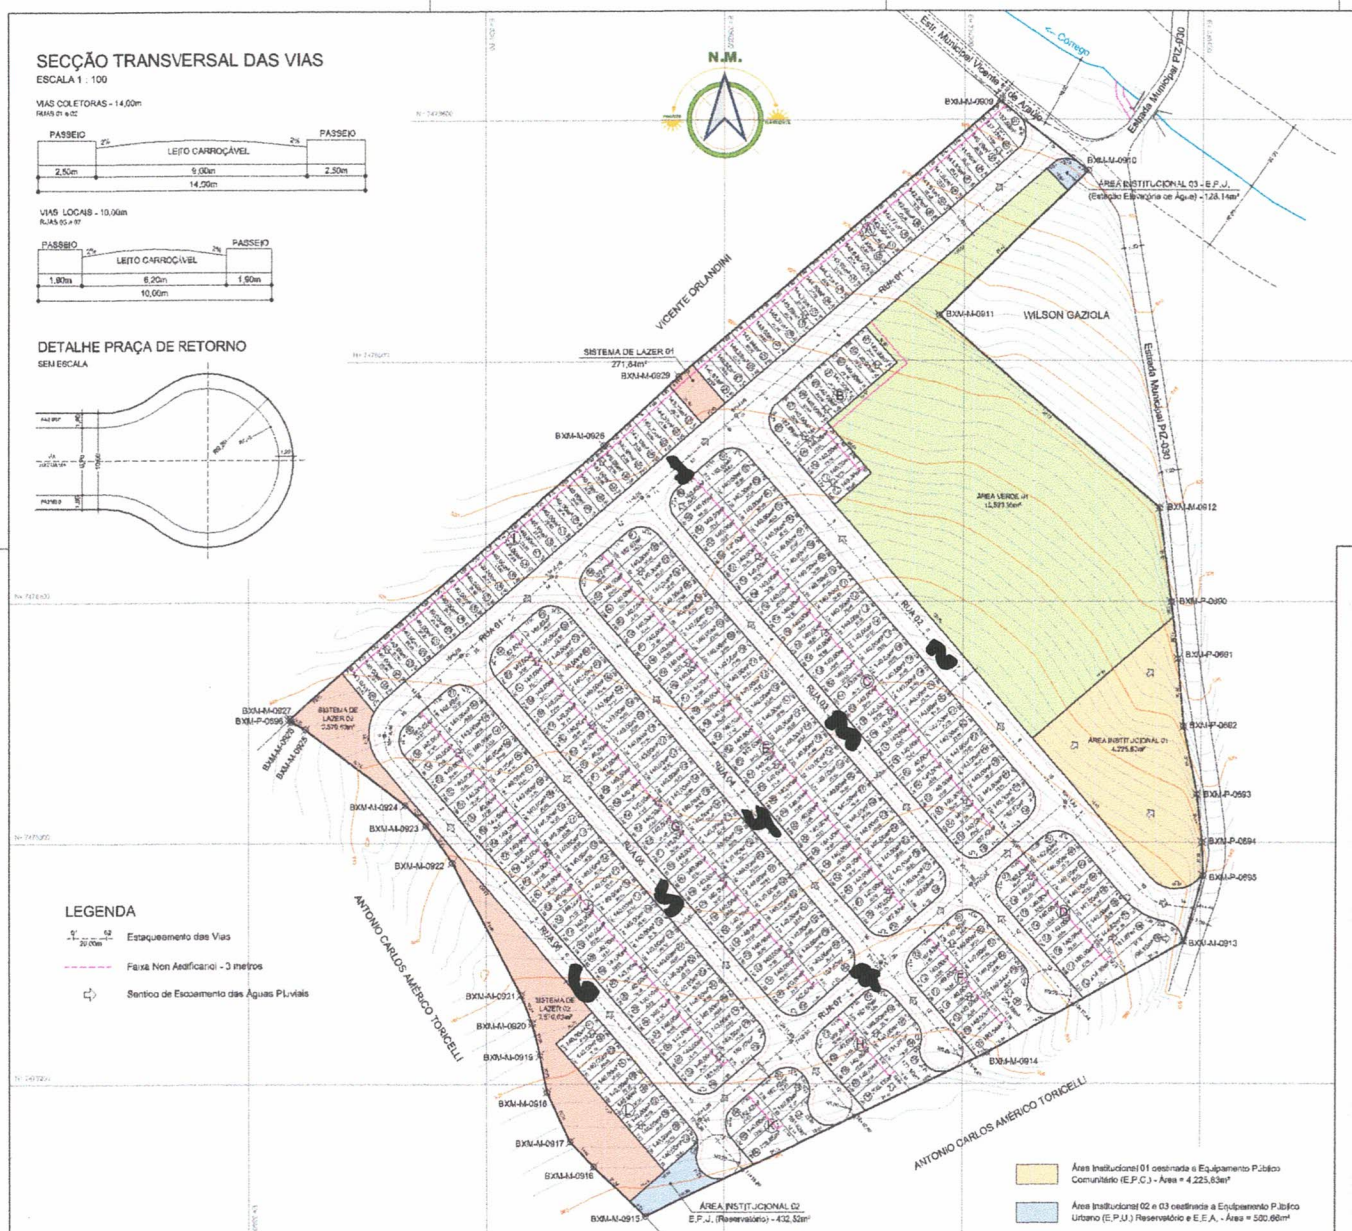

LEGENDA

- Estaqueamento das Vias
- Faixa Non Aedificandi - 3 metros
- Sentido de Escoamento das Águas Pluviais

PERÍMETRO

DE	PARA	AZIMUTE	DISTÂNCIA
BXM-M-0909	BXM-M-0910	128°32'38"	46,84
BXM-M-0910	BXM-M-0911	226°27'05"	86,52
BXM-M-0911	BXM-M-0912	131°01'47"	122,79
BXM-M-0912	BXM-P-0690	172°43'51"	39,27
BXM-P-0690	BXM-P-0691	173°58'29"	23,77
BXM-P-0691	BXM-P-0692	175°13'32"	26,22
BXM-P-0692	BXM-P-0693	166°38'50"	28,61
BXM-P-0693	BXM-P-0694	173°38'08"	20,17
BXM-P-0694	BXM-P-0695	178°11'15"	13,89
BXM-P-0695	BXM-M-0913	196°42'23"	28,54
BXM-M-0913	BXM-M-0914	241°04'27"	94,50
BXM-M-0914	BXM-M-0915	244°51'41"	158,87
BXM-M-0915	BXM-M-0916	313°58'47"	30,10
BXM-M-0916	BXM-M-0917	316°32'18"	14,42
BXM-M-0917	BXM-M-0918	335°13'51"	20,75
BXM-M-0918	BXM-M-0919	349°00'32"	13,63
BXM-M-0919	BXM-M-0920	345°40'35"	13,66
BXM-M-0920	BXM-M-0921	338°41'13"	12,70
BXM-M-0921	BXM-M-0922	332°54'32"	61,88
BXM-M-0922	BXM-M-0923	324°37'47"	18,91
BXM-M-0923	BXM-M-0924	314°04'22"	12,08
BXM-M-0924	BXM-M-0926	306°42'13"	32,75
BXM-M-0926	BXM-M-0926	299°18'45"	6,74
BXM-M-0926	BXM-P-0696	298°37'48"	1,47
BXM-P-0696	BXM-M-0927	47°55'34"	1,03
BXM-M-0927	BXM-M-0928	49°35'49"	173,84
BXM-M-0928	BXM-M-0929	48°02'13"	42,41
BXM-M-0929	BXM-M-0909	49°46'47"	176,36

Matrícula 73.586 Área Total = 95.284,47m²

PROJETO URBANÍSTICO

FOLHA ÚNICA

PROJETO LOTEAMENTO RESIDENCIAL VISTA DOS PINHEIROS II

PROPRIETÁRIO PINHAL 2 - EMPREENDIMENTOS SPE LTDA
CNPJ nº 28.044.516/0001-61

LOCAL Estrada Municipal Vicente de Araújo
Bairro do Matão - Pinhalzinho - SP

ESCALA 1:1000

MATRÍCULA nº 73.586 DO C.R.I DA COMARCA DE BRAGANÇA PAULISTA-SP

SITUAÇÃO SEM ESCALA

VIDE PLANTA

DECLARAÇÃO

DECLARO QUE A APROVAÇÃO DO PROJETO NÃO IMPLICA A PREFEITURA NO RECONHECIMENTO DO DIREITO DE PROPRIEDADE NO REFERIDO IMÓVEL

PINHAL 2 - EMPREENDIMENTOS SPE LTDA
ANDRÉ TOSCANO BONDANÇA
CPF nº 455.855.758-00

ÁREAS

	m²	%
1. ÁREA DOS LOTES		
1.1. LOTES RESIDENCIAIS (1427 UHs)	45.309,74	51,75
2. ÁREAS PÚBLICAS		
2.1. SISTEMA VIÁRIO	21.521,82	22,31
2.2. ÁREA INSTITUCIONAL (Total Uni. e Comun.)	4.755,49	5,00
2.3. ESPAÇOS LIVRES DE USO PÚBLICO		
2.3.1. ÁREAS VERDES	16.032,96	16,25
2.3.2 SISTEMA DE LAZER	3.842,47	4,05

MARCOS ROBERTO GUARIZZO
ENGENHEIRO CIVIL
CREA 060286220

VISTO PRÉVIO
PREFEITURA MUNICIPAL
DE PINHALZINHO
30 / 11 / 2020

Vinculado a validade de conformidade deste empreendimento emitida em 30/11/2020