# LEI Nº 1894/2024
# DE 23 de ABRIL DE 2024

**"Dispõe sobre denominação de via pública e dá outras providências."**

**PAULO ROGÉRIO PEREIRA**, no exercício do cargo de Prefeito Municipal, no uso das atribuições que lhe são conferidas por Lei, faz saber que a Câmara Municipal aprovou e eu sanciono a seguinte Lei:

**Artigo 1º** - A rua 1 do Loteamento denominado "Fazenda Bela Manhã", situado no Bairro da Fazenda Velha, conforme mapa em anexo, passa a denominar-se:

**- Rua Bela Manhã.**

**Artigo 2º** - Esta Lei entra em vigor na data de sua publicação, revogadas as disposições em contrário.

Pinhalzinho/SP, 23 de abril de 2024.

**PAULO ROGÉRIO PEREIRA**

**PREFEITO MUNICIPAL DE PINHALZINHO/SP**

**Publicado no Diário Oficial do Município em 08/05/2024 – Edição nº 818/2024**

## Matrícula 64.190

| De | Para | Rumo | Distância |
|---|---|---|---|
| MC1 | MC2 | 21°08'28"SW | 62,720m |
| MC2 | MC3 | 20°07'56"SW | 132,701m |
| MC3 | MC4 | 79°25'31"SE | 35,942m |
| MC4 | MC5 | 89°35'07"NE | 90,626m |
| MC5 | MC6 | 83°06'50"NE | 32,078m |
| MC6 | MC7 | 05°18'06"NE | 55,032m |
| MC7 | MC8 | 16°18'19"NE | 45,677m |
| MC8 | MC9 | 28°26'06"NE | 38,412m |
| MC9 | MC10 | 34°47'50"NE | 26,659m |
| MC10 | MC1 | Estrada Municipal | 149,33m |

Área: 26.750,96m

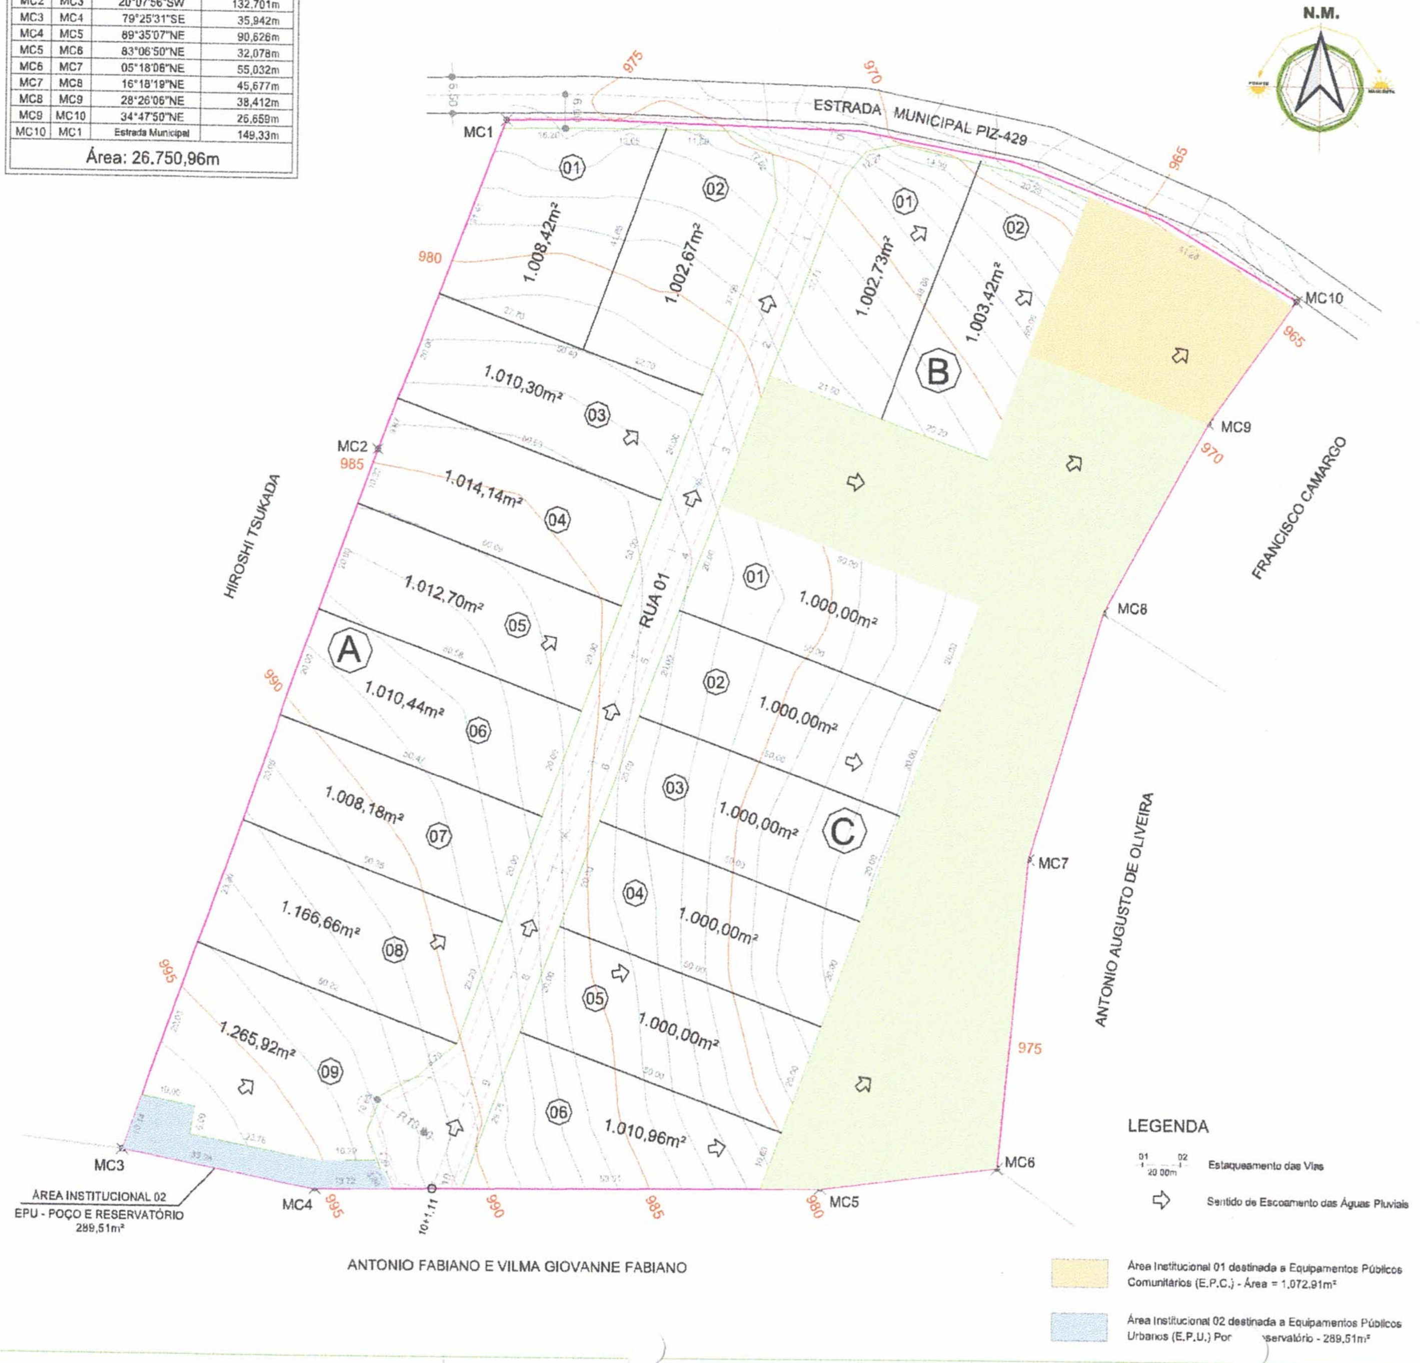

## DETALHE PRAÇA DE RETORNO

SEM ESCALA

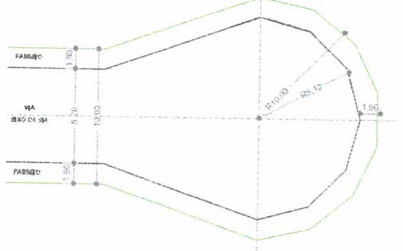

VIA LOCAL - 10,00m

RUA 01

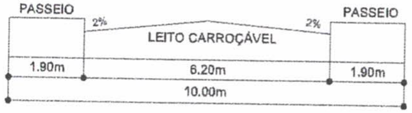

## PROJETO URBANÍSTICO

FOLHA ÚNICA

PROJETO LOTEAMENTO "FAZENDA BELA MANHÃ"

PROPRIETÁRIO CONSTRUTORA POR DO SOL LTDA.
CNPJ nº 32.469.031/0001-82

LOCAL Estrada Municipal PIZ-429
Bairro da Fazenda Velha - Pinhalzinho-SP

ESCALA 1:500 Matrícula nº 64.190 do Cartório de Registro de Imóveis de Bragança Paulista-SP

### SITUAÇÃO SEM ESCALA

VIDE PROJETO

### DECLARAÇÃO

DECLARO QUE A APROVAÇÃO DO PROJETO NÃO IMPLICA A PREFEITURA NO RECONHECIMENTO DO DIREITO DE PROPRIEDADE NO REFERIDO IMÓVEL

PROPRIETÁRIO
CONSTRUTORA POR DO SOL LTDA.
CNPJ [illegible]
MÁRCIO MARTINS DE ALMEIDA
CPF [illegible]

AUTOR DO PROJETO E RESP. TÉCNICO
MARCOS ROBERTO GUARIZZO
ENGENHEIRO CIVIL
CREA [illegible]
ART [illegible]

| ÁREAS | m² | % |
|---|---|---|
| 1. ÁREA DOS LOTES | | |
| 1.1. LOTES RESIDENCIAIS (17 unid.) | 17.516,54 | 65,48 |
| 2. ÁREAS PÚBLICAS | | |
| 2.1. SISTEMA VIÁRIO | 2.511,71 | 9,39 |
| 2.2. ÁREA INSTITUCIONAL (Equip. Urb. e Comun.) | 1.362,42 | 5,09 |
| 2.3. ESPAÇOS LIVRES DE USO PÚBLICO | | |
| 2.3.1 ÁREAS VERDES | 5.360,29 | 20,04 |
| TOTAL DA GLEBA = ÁREA LOTEADA | 26.750,96 | 100,00 |