-

LEI Nº 1912/2024
DE 16 DE JULHO DE 2024

"Dispõe sobre denominação de vias públicas que específica"

PAULO ROGÉRIO PEREIRA, no exercício do cargo de Prefeito Municipal, no uso das atribuições que lhe são conferidas por Lei, faz saber que a **CÂMARA MUNICIPAL** aprovou e eu sanciono a seguinte Lei:

Artigo 1º - As ruas do Loteamento Chácaras Recanto do Sol passam a denominar-se:

Rua 01 – Reinaldo Garcia (Baixinho);
Rua 02 – José Aparecido Franco (Zitão);
Rua 03 – Ana Gusson Franco;
Rua 04 – Isaura Ribeiro Zanardi;
Rua 05 – José Zanardi; e
Rua 06 – Maria de Lourdes de Freitas Bacci.

Artigo 2º - Esta Lei entra em vigor na data de sua publicação, revogadas as disposições em contrário.

Pinhalzinho/SP, 16 de julho de 2024

PAULO ROGÉRIO PEREIRA
Prefeito Municipal de Pinhalzinho/SP

Publicado no Diário Oficial do Município em 16/07/2024 – Edição 883/2024

PROJETO URBANÍSTICO

10153-

FOLHA ÚNICA

PROJETO — LOTEAMENTO CHÁCARAS RECANTO DO SOL

PROPRIETÁRIO — ALEXANDRE MARCEL FRANCO E OUTROS
ZANARDI EMPREENDIMENTOS IMOBILIÁRIOS LTDA.

LOCAL — ESTRADA MUNICIPAL PIZ-351 - GLEBA 01 E GLEBA 02
BAIRRO DO PINHAL - PINHALZINHO-SP

ESCALA 1:1000

MATRÍCULAS nº 98.397 e nº 98.404 DO C.R.I. DA COMARCA DE BRAGANÇA PAULISTA

SITUAÇÃO SEM ESCALA

VIDE PLANTA

ÁREAS	m²	%
1. ÁREA DOS LOTES		
1.1. LOTES RESIDENCIAIS (102 unid.)	108.436,02	55,41
2. ÁREAS PÚBLICAS		
2.1. SISTEMA VIÁRIO	20.243,34	10,35
2.2. ÁREA INSTITUCIONAL (equip. urbanos e san.)	12.356,63	6,31
2.3. ESPAÇOS LIVRES DE USO PÚBLICO		
2.3.1 ÁREAS VERDES	54.648,32	27,93
ÁREA LOTEADA = TOTAL DA GLEBA	195.684,31	100,00

DECLARAÇÃO

DECLARO QUE A APROVAÇÃO DO PROJETO NÃO IMPLICA A PREFEITURA NO RECONHECIMENTO DO DIREITO DE PROPRIEDADE NO REFERIDO IMÓVEL

PROPRIETÁRIO
ALEXANDRE MARCEL FRANCO
CPF 249.342.798-06

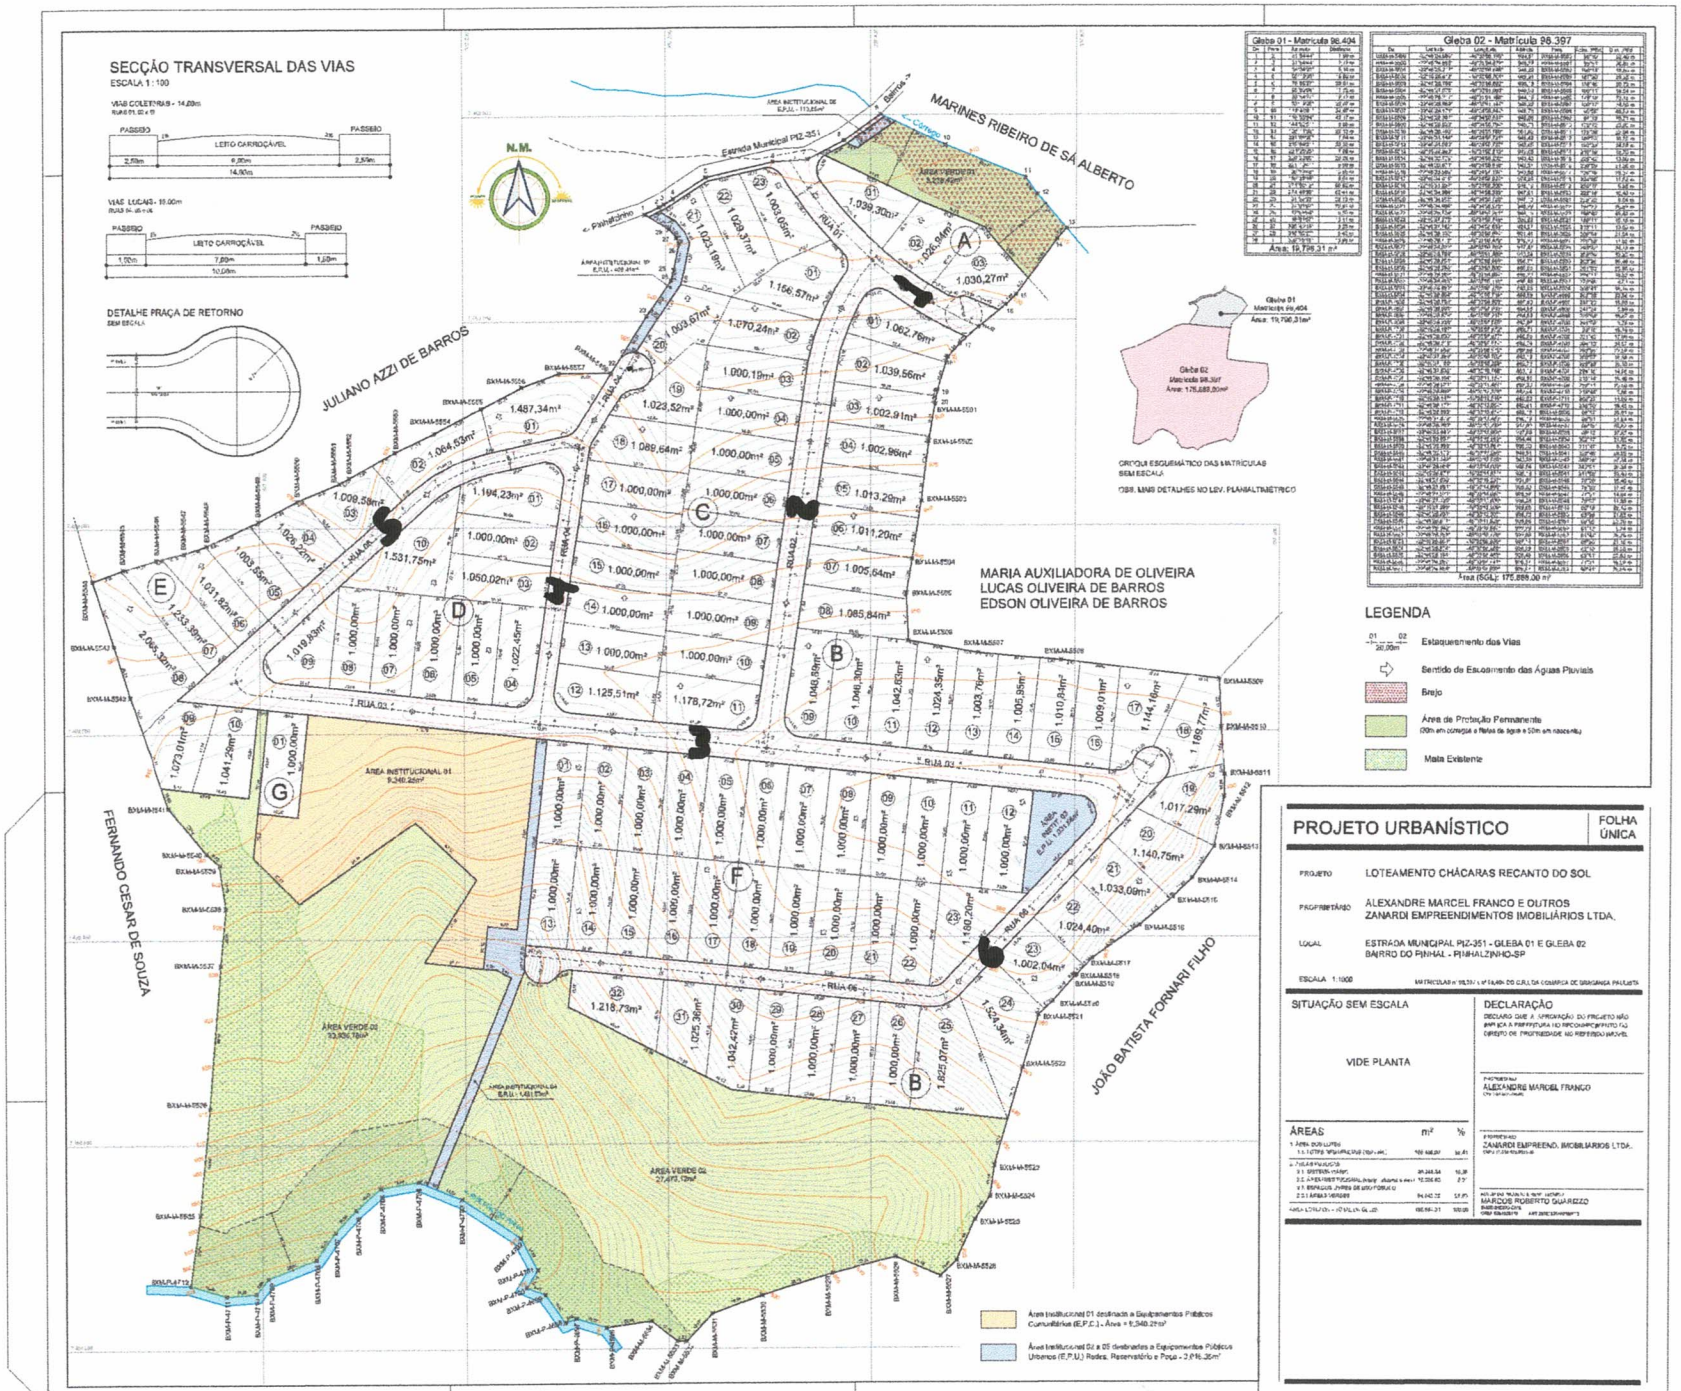
PROPRIETÁRIO
ZANARDI EMPREEND. IMOBILIÁRIOS LTDA.
CNPJ 16.518.462/0001-35

AUTOR DO PROJETO E RESP. TÉCNICO
MARCOS ROBERTO GUARIZZO
ENGENHEIRO CIVIL
CREA 5061638170 ART 28027230190196712

APROVADO
EM 06/11/2019
PREFEITURA MUNICIPAL DE PINHALZINHO

Edson Lisboa Santos
ARQUITETO & URBANISTA
CAU - A88566-9
CHEFE DEPTO. OBRAS

graprohab
APROVADO
Certificado nº 308/19
Lacir Ferreira Baldusco
Presidente


SECÇÃO TRANSVERSAL DAS VIAS
ESCALA 1 : 100
VIAS COLETORAS - 14,00m
RUAS 01, 02 e 03
PASSEIO
LEITO CARROÇÁVEL
2,50m
6,00m
2,50m
14,00m
VIAS LOCAIS - 10,00m
RUAS 04, 05 e 06
1,00m
7,00m
10,00m
DETALHE PRAÇA DE RETORNO
SEM ESCALA
N.M.
MARINES RIBEIRO DE SÁ ALBERTO
Estrada Municipal PIZ-351
Córrego
Ribeirão do Pinhal
JULIANO AZZI DE BARROS
FERNANDO CESAR DE SOUZA
JOÃO BATISTA FORNARI FILHO
MARIA AUXILIADORA DE OLIVEIRA
LUCAS OLIVEIRA DE BARROS
EDSON OLIVEIRA DE BARROS
RUA 01
RUA 02
RUA 03
RUA 04
RUA 05
RUA 06
ÁREA INSTITUCIONAL 01
9.240,26m²
ÁREA VERDE 01
3.239,49m²
ÁREA VERDE 02
33.926,78m²
ÁREA VERDE 03
27.473,10m²
ÁREA INSTITUCIONAL 02
E.P.U. - 1.451,35m²
ÁREA INSTITUCIONAL 03
E.P.U. - 1.701,84m²
Área Institucional 01 destinada a Equipamentos Públicos Comunitários (E.P.C.) - Área = 9.240,26m²
Área Institucional 02 e 03 destinadas a Equipamentos Públicos Urbanos (E.P.U.) Redes, Reservatório e Poço - 3.153,35m²
Gleba 01 - Matrícula 98.404
Área: 19.796,31m²
Gleba 02 - Matrícula 98.397
Área (SGL): 175.888,00 m²
Área: 19.796,31 m²
Gleba 01
Matrícula 98.404
Área: 19.796,31m²
Gleba 02
Matrícula 98.397
Área: 175.888,00m²
CROQUI ESQUEMÁTICO DAS MATRÍCULAS
SEM ESCALA
ISBN, MMS DETALHES NO LEV. PLANIALTIMÉTRICO
LEGENDA
Estaqueamento das Vias
Sentido de Escoamento das Águas Pluviais
Brejo
Área de Proteção Permanente
(30m em corrego e Raios de água e 50m em nascentes)
Mata Existente
PROJETO URBANÍSTICO
FOLHA ÚNICA
PROJETO
LOTEAMENTO CHÁCARAS RECANTO DO SOL
PROPRIETÁRIO
ALEXANDRE MARCEL FRANCO E OUTROS
ZANARDI EMPREENDIMENTOS IMOBILIÁRIOS LTDA.
LOCAL
ESTRADA MUNICIPAL PIZ-351 - GLEBA 01 E GLEBA 02
BAIRRO DO PINHAL - PINHALZINHO-SP
ESCALA 1:1000
SITUAÇÃO SEM ESCALA
VIDE PLANTA
DECLARAÇÃO
ÁREAS
m²
%
ALEXANDRE MARCEL FRANCO
ZANARDI EMPREEND. IMOBILIÁRIOS LTDA.
MARCOS ROBERTO GUARIZZO