LEI Nº 1.924/2024
DE 19 DE SETEMBRO DE 2024

"Dispõe sobre denominação de vias públicas que especifica"

PAULO ROGÉRIO PEREIRA, no exercício do cargo de Prefeito Municipal, no uso das atribuições que lhe são conferidas por Lei, faz saber que a Câmara Municipal aprovou e eu sanciono a seguinte Lei:

Artigo 1º - As ruas do Loteamento Residencial Alto das Estrelas, localizado no Bairro da Fazenda Velha, neste Município, passam a denominar-se:

Rua 01 – Júpiter;
Rua 02 – Plutão;
Rua 03 – Vênus;
Rua 04 – Saturno; e
Rua 05 – Marte.

Artigo 2º - Esta Lei entra em vigor na data de sua publicação, revogadas as disposições em contrário.

Pinhalzinho, 19 de setembro de 2024.

PAULO ROGÉRIO PEREIRA
Prefeito Municipal

Publicado no Diário Oficial do Município em 20/09/2024 – Edição 943/2024

PROJETO URBANÍSTICO

FOLHA 03/03

TITULO: REGULARIZAÇÃO FUNDIÁRIA

DENOMINAÇÃO: ALTO DAS ESTRELAS

PROPRIETÁRIO: SEBASTIÃO ZANARDI

LOCALIZAÇÃO: ESTRADA MUNICIPAL
BAIRRO DA FAZENDA VELHA
MUNICÍPIO DE PINHALZINHO
SÃO PAULO

ÁREAS

TOTAL LOTES (79)	88.389,57 m2	73,06%
ÁREAS PÚBLICAS		
ÁREA INSTITUCIONAL	7.141,19 m2	5,90%
SISTEMA VIÁRIO	17.702,88 m2	14,22%
ESPAÇOS LIVRES DE USO PÚBLICO		
SISTEMA DE LAZER	8.254,80 m2	6,82%
TOTAL ÁREAS PÚBLICAS	32.598,87 m2	26,94%
ÁREA LOTEADA	120.988,44 m2	100,00%
TOTAL GLEBA	120.988,44 m2	

Proprietário
SEBASTIÃO ZANARDI

Resp. Técnico
Engº Civil MARCOS ROBERTO GUARIZZO
C.R.E.A. 5061638170


Prefeitura Municipal de Pinhalzinho

REGULARIZADO

Nº DO PROCESSO: —
APROVAÇÃO: 01/2018
DATA: 25/09/2018
RESPONSÁVEL:

Edson Lisboa Santos
ARQUITETO & URBANISTA
CAU - A68556-9
SECRETÁRIO MUNICIPAL DE
OBRAS E SERVIÇOS PÚBLICOS

ESCALA
1 : 1.000

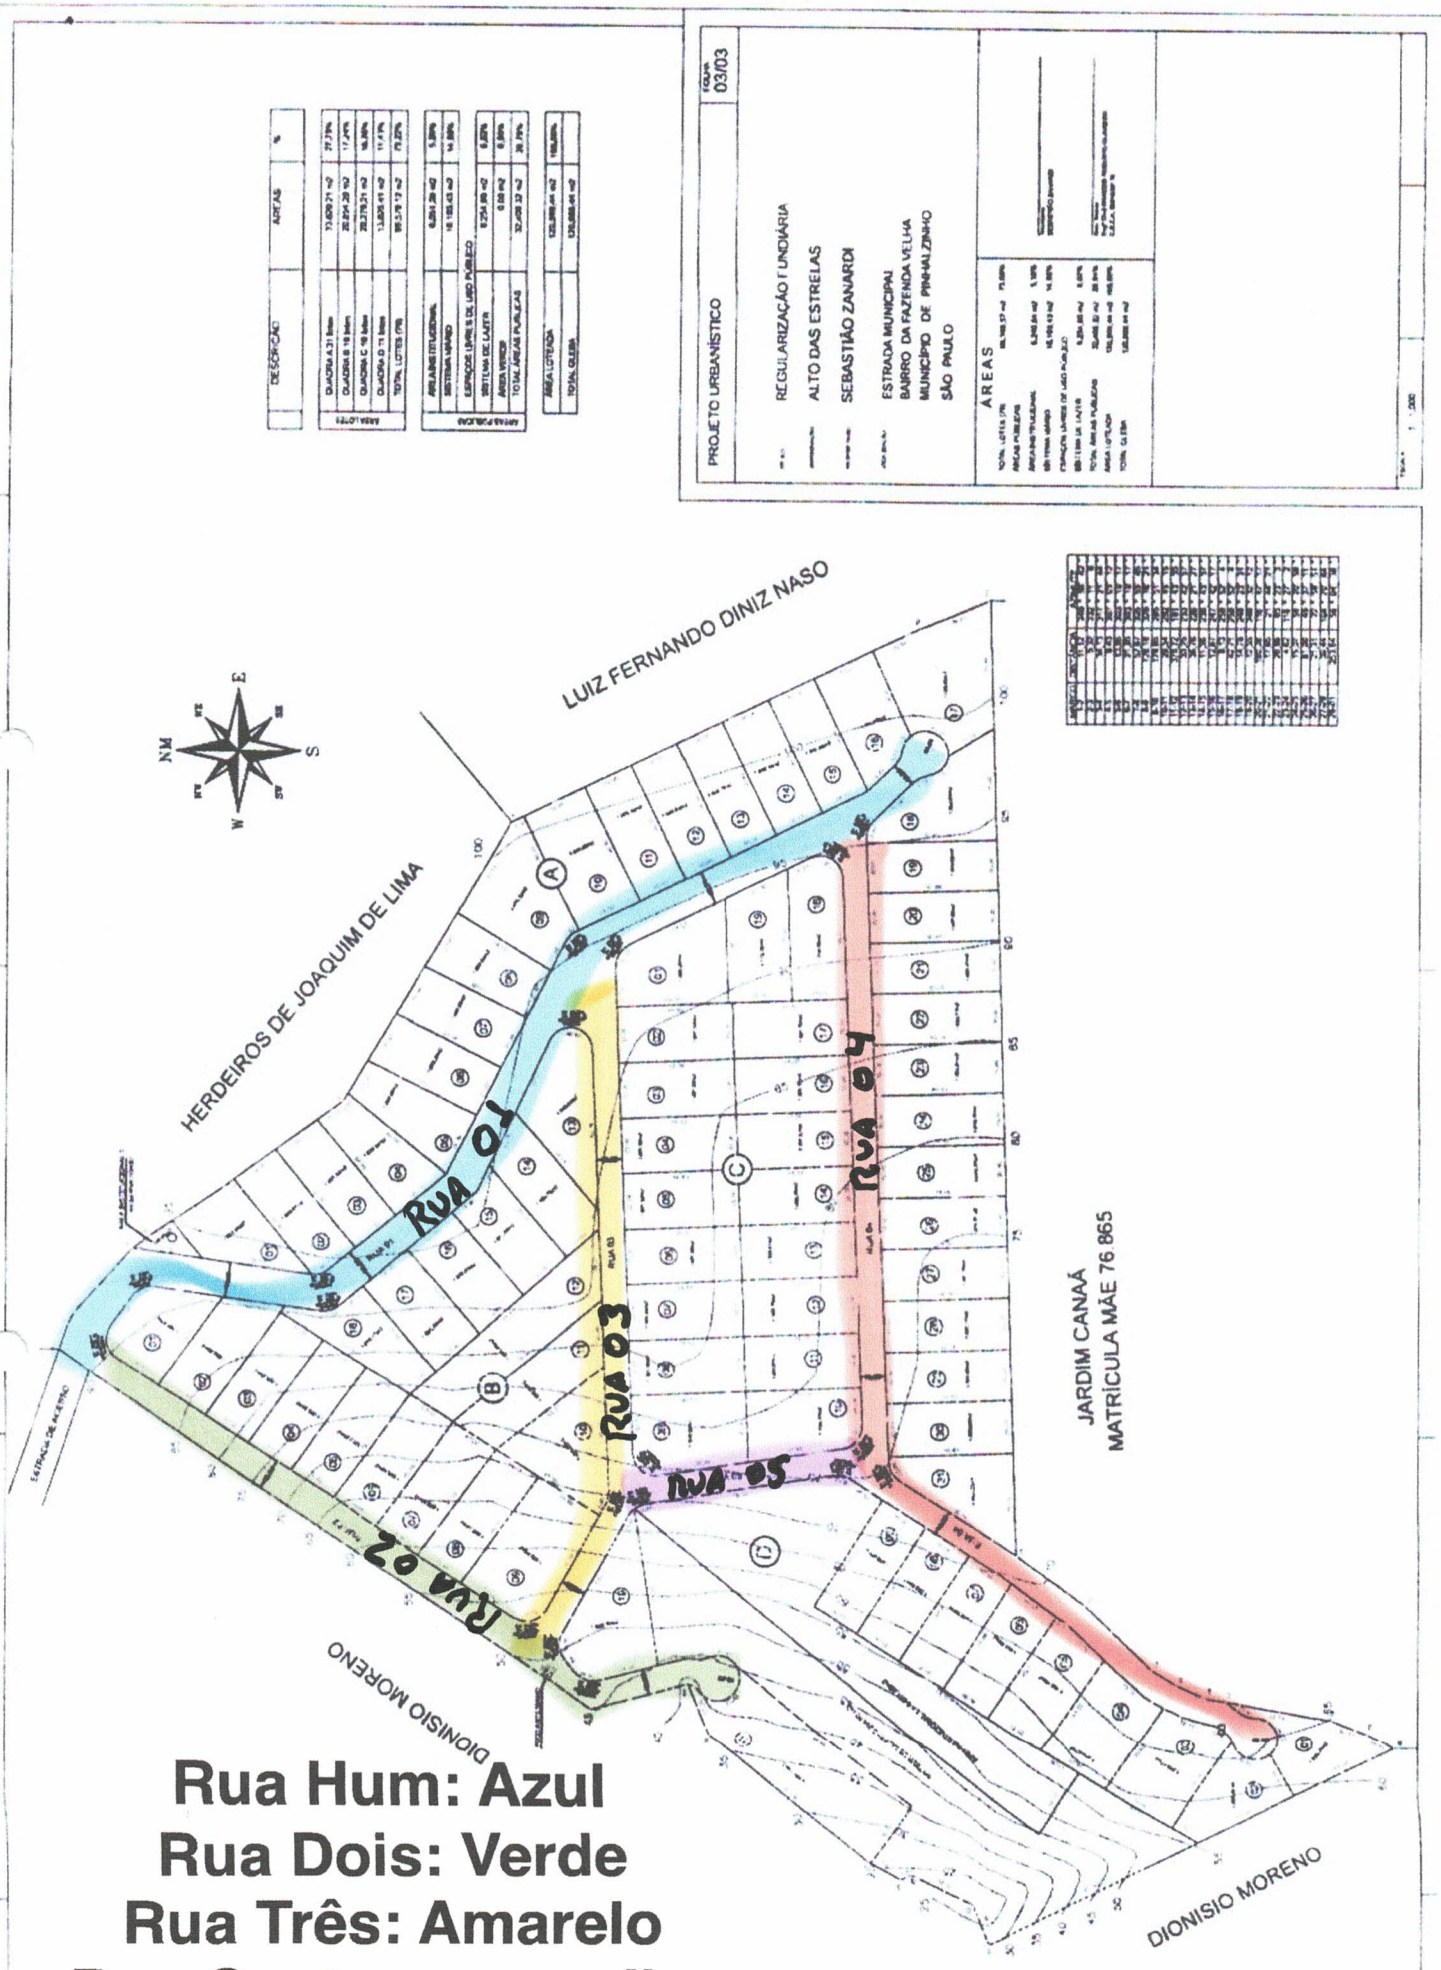

Rua Hum: Azul

Rua Dois: Verde

Rua Três: Amarelo

Rua Quatro: vermelho

Rua Cinco: Roxo